

Alcance de los Trabajos

Calle San Miguel 22, Santa Cruz de Tenerife

El presente alcance de los trabajos deberá leerse conjuntamente con los últimos planos de Arquitectura, Estructura y Estructura Metálica.

1. Trabajos Preliminares

- Incluir todos los trabajos provisionales necesarios para la ejecución del proyecto, incluyendo implantación de obra, protecciones, andamios, gestión de residuos y limpieza.
- Obtener y coordinar todos los permisos, licencias y autorizaciones necesarios para el acceso a la obra, ocupación de la vía pública, andamios, contenedores, entregas, operaciones de elevación y demás trabajos provisionales asociados a los trabajos del Contratista.

2. Demoliciones

Ejecutar todas las demoliciones indicadas en los planos, incluyendo:

- Forjados de cubierta y de plantas.
- Muros de mampostería.
- Enlucidos y acabados donde sea necesario.
- Retirada y gestión de los residuos de demolición.

3. Trabajos Estructurales

Ejecutar todos los trabajos estructurales indicados en los planos, incluyendo:

- Apeos provisionales.
- Refuerzo de la mampostería existente.
- Estructura metálica.
- Trabajos estructurales de hormigón armado.
- Nuevos forjados de cubierta y de plantas.
- Hueco en la cubierta para la escalera.

4. Mampostería y Huecos

Ejecutar todos los trabajos de mampostería indicados en los planos, incluyendo:

- Nueva mampostería.
- Modificaciones de la mampostería existente.
- Nuevos huecos y modificaciones de huecos existentes para puertas y ventanas.
- Nuevos dinteles.
- Huecos y pasos necesarios para las instalaciones.

5. Trabajos de Cubierta

Ejecutar el sistema completo de cubierta, incluyendo:

- Impermeabilización.
- Aislamiento térmico.
- Formación de pendientes.
- Evacuación de aguas pluviales, incluyendo sumideros y bajantes desde la cubierta hasta la red de desagüe existente.

6. Escalera Metálica

La escalera metálica será suministrada por la Propiedad.

El Contratista deberá instalar la escalera, construir el cerramiento de acceso a la cubierta y realizar todos los trabajos de albañilería asociados.

7. Ventanas y Puertas Exteriores

Instalar todas las ventanas y puertas exteriores suministradas por la Propiedad.

Proteger todas las ventanas y puertas exteriores suministradas por la Propiedad durante la ejecución de las obras. Cualquier elemento dañado deberá ser sustituido por el Contratista.

8. Enlucidos y Reparaciones

Realizar todos los trabajos de enlucido y reparación necesarios tras los trabajos estructurales, incluyendo reparaciones de paredes interiores, paredes exteriores y fachada.


9. Exclusiones

Salvo que se indique expresamente lo contrario, quedan excluidos:


- Diseño y fabricación de la escalera metálica.
- Instalación eléctrica.
- Fontanería.
- Climatización.
- Cocina.
- Baños.
- Puertas interiores.
- Acabados de suelos.
- Acabados de paredes.
- Electrodomésticos.

10. General


El Contratista deberá incluir toda la mano de obra, materiales, maquinaria, trabajos provisionales, fijaciones y trabajos auxiliares necesarios para completar las obras de acuerdo con los planos.

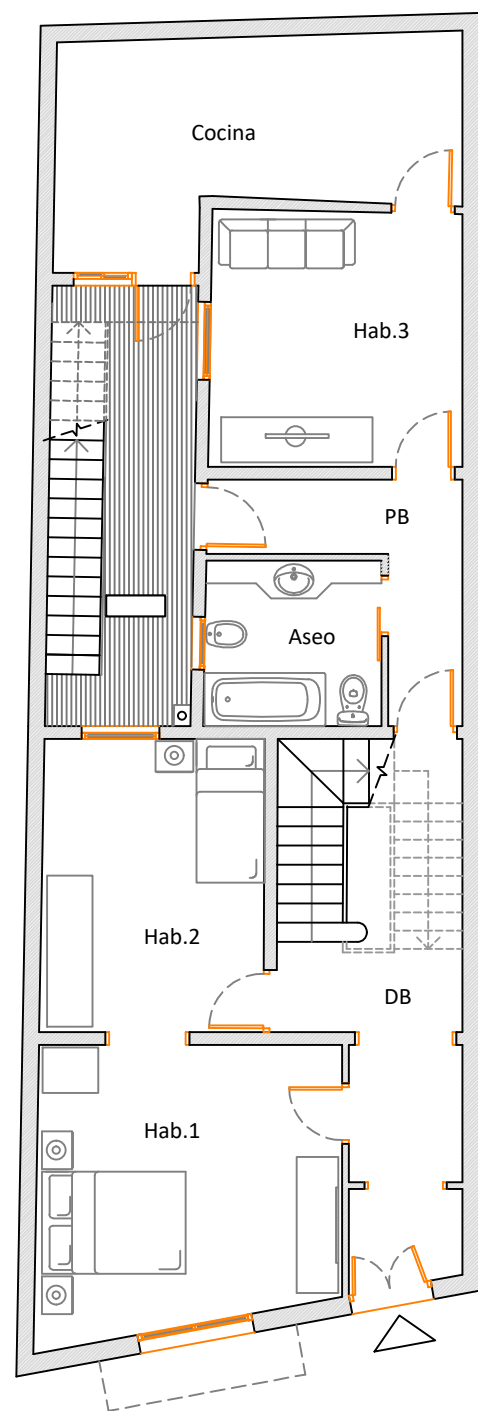


Planta baja

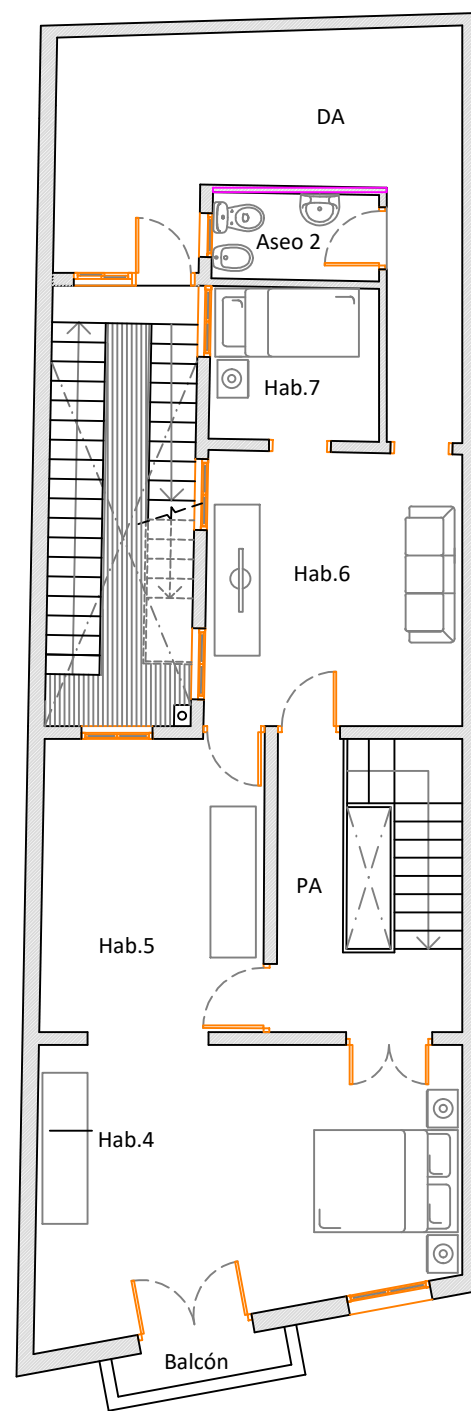

Planta alta

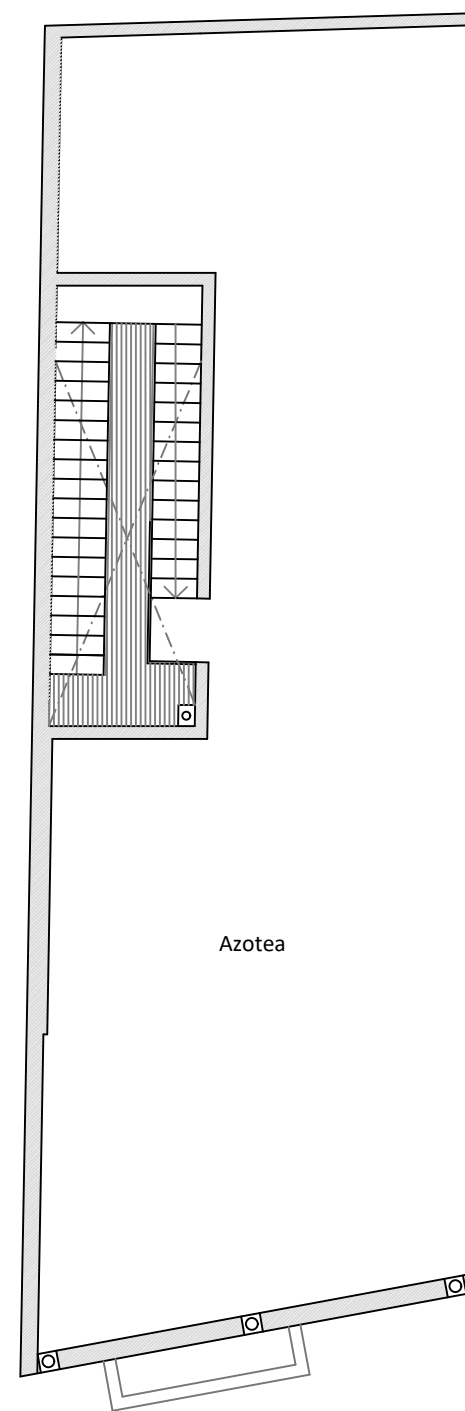

Planta cubierta

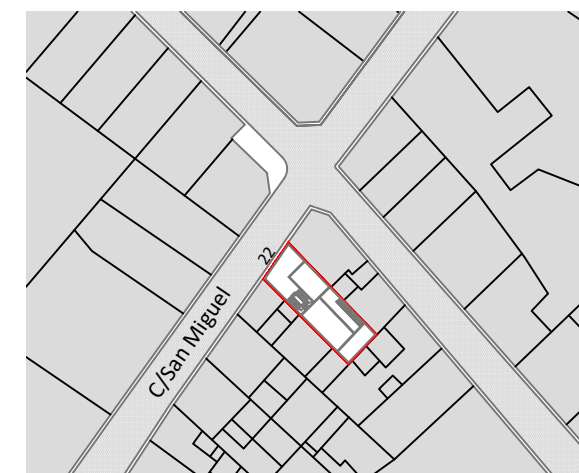

Ordenación propuesta

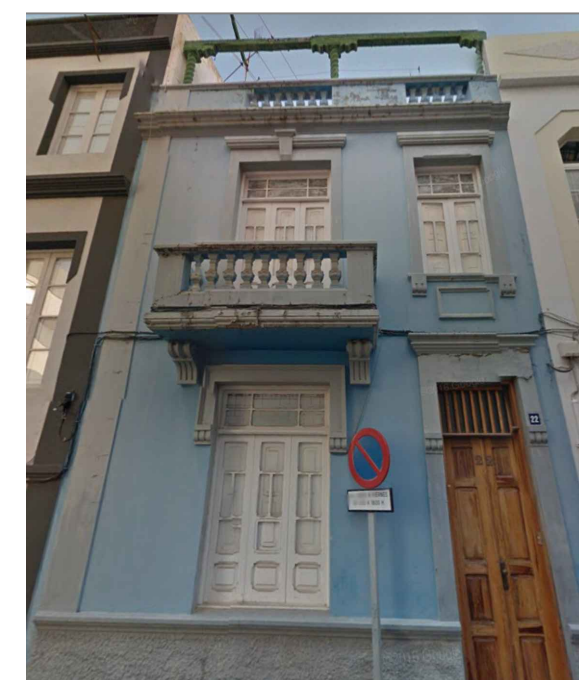


Foto del inmueble

FERNANDO GARCIA ORTEGA

C/ Cruz verde, 21-23 3ª Planta Oficina O - 38003 Santa Cruz de Tenerife - telefono: 670 244 678 - fernando@calcularq.com

arquitecto

Demolición y reposición de forjado
y nuevo acceso a cubierta

Plantas estado Actual plano nº

03

C/ San Miguel nº22 - CP:38002








escala

Septiembre 2016

sustituye

María Belén Lerena Guil - Alessandro Evangelista

propiedad

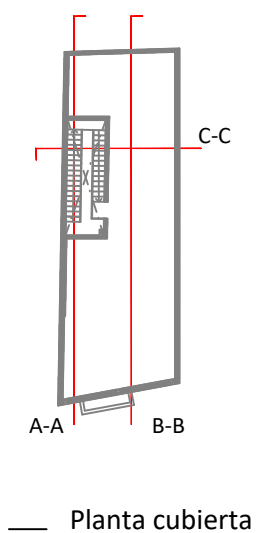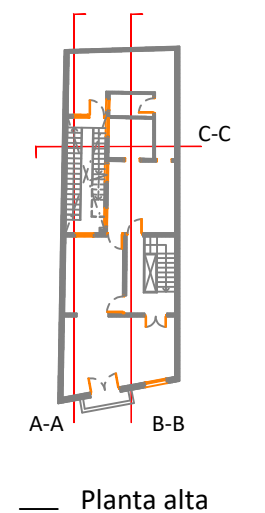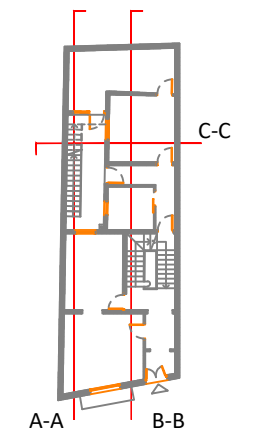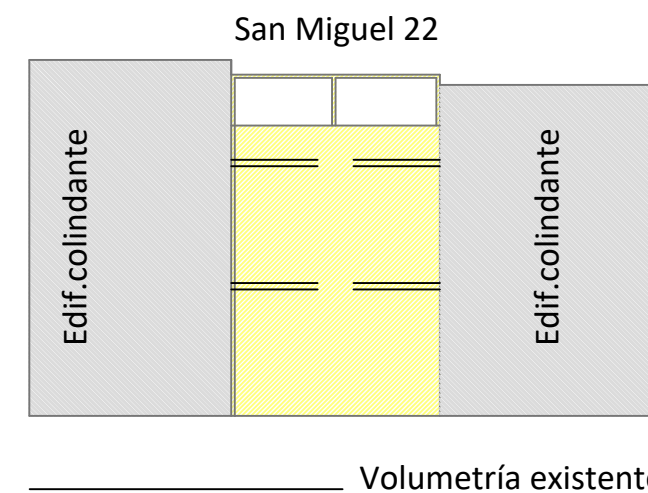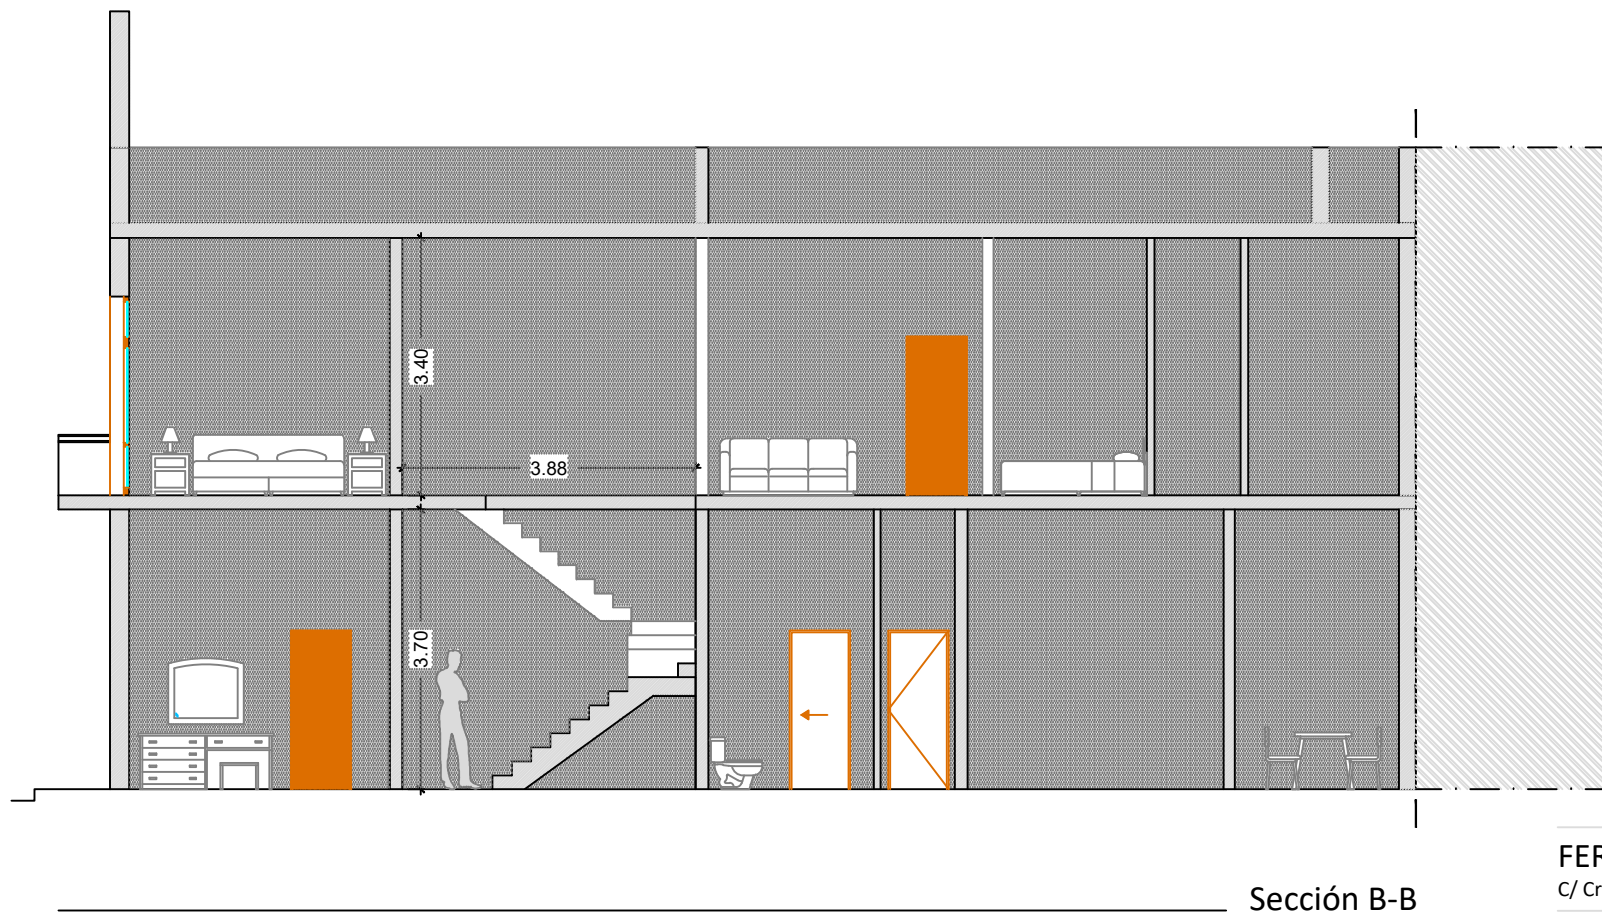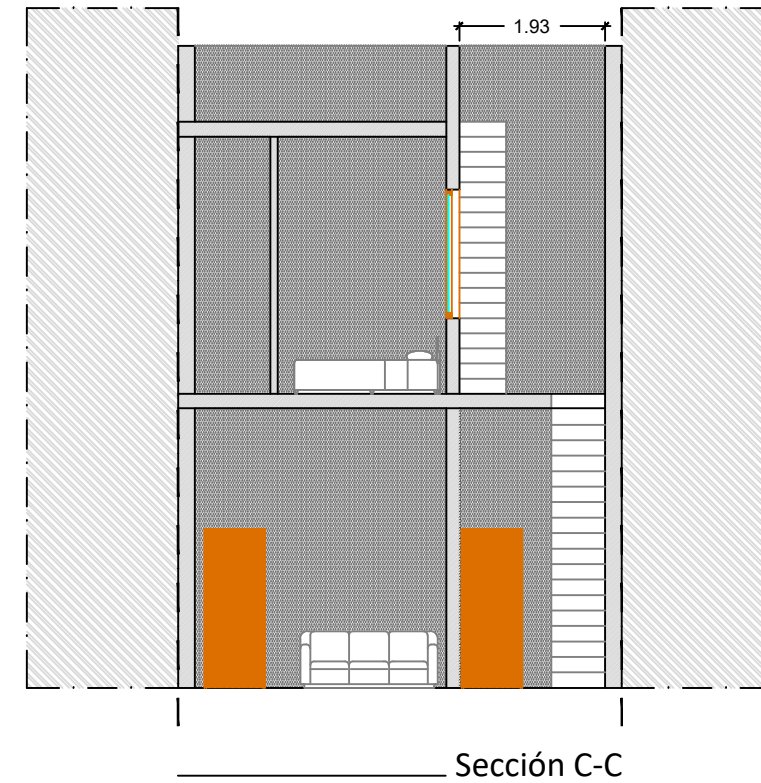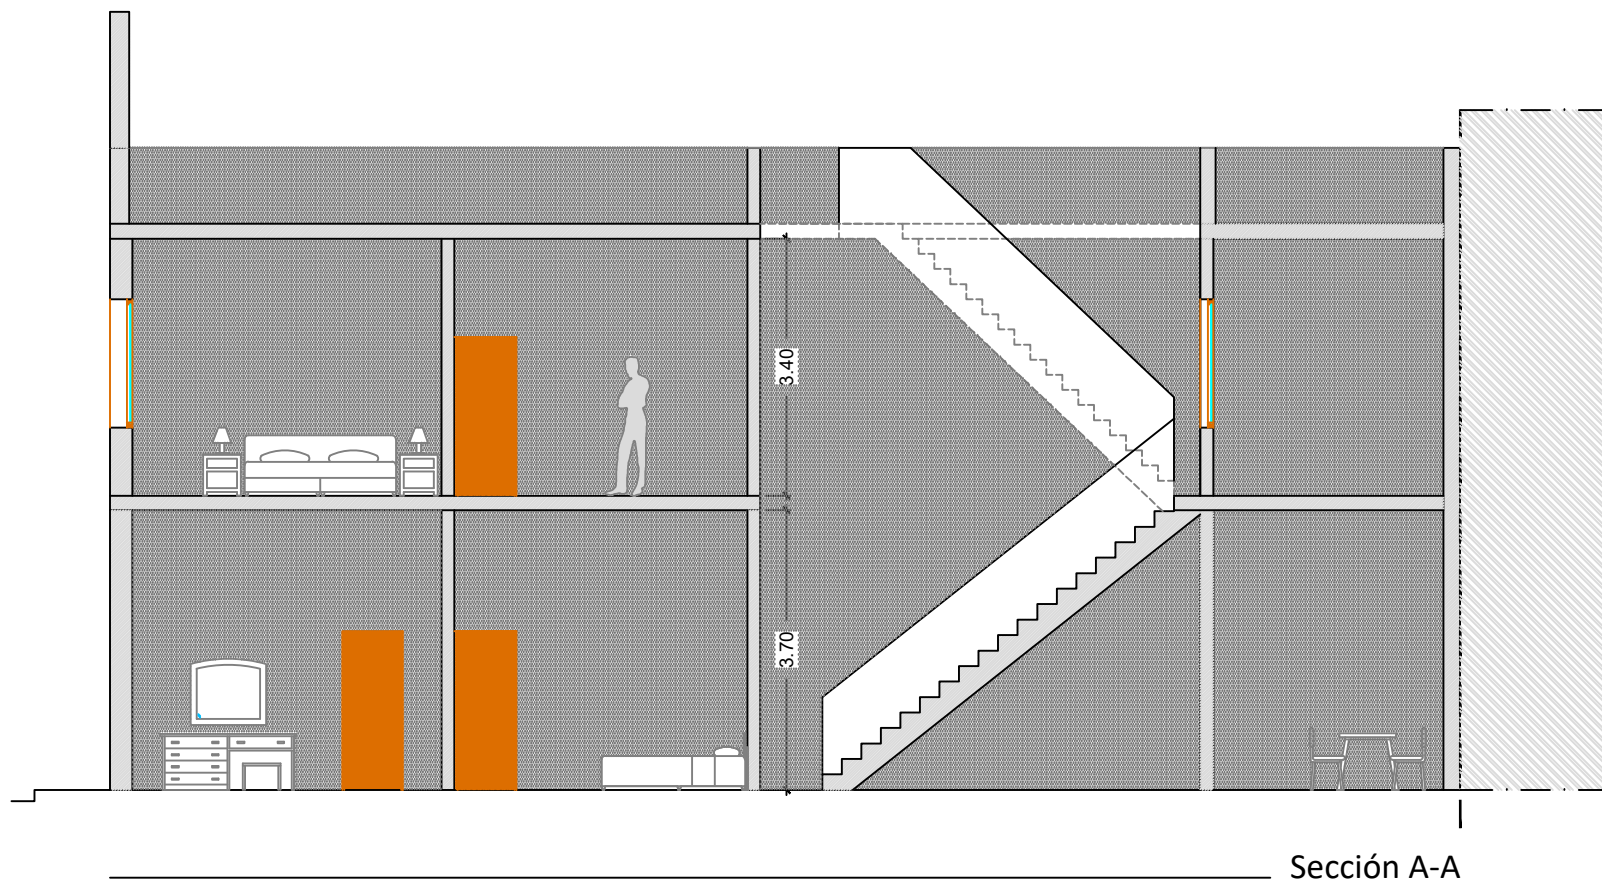

FERNANDO GARCIA ORTEGA

C/ Cruz verde, 21-23 3ª Planta Oficina O - 38003 Santa Cruz de Tenerife - telefono: 670 244 678 - fernando@calcularq.com

arquitecto

Demolición y reposición de forjado y nuevo acceso a cubierta

Secciones estado actual

plano nº

04

C/ San Miguel nº22 - CP:38002

escala


Septiembre 2016

sustituye


María Belén Lerena Guil - Alessandro Evangelista

propiedad


Límite edificación Área seccionada Edif.colindantes

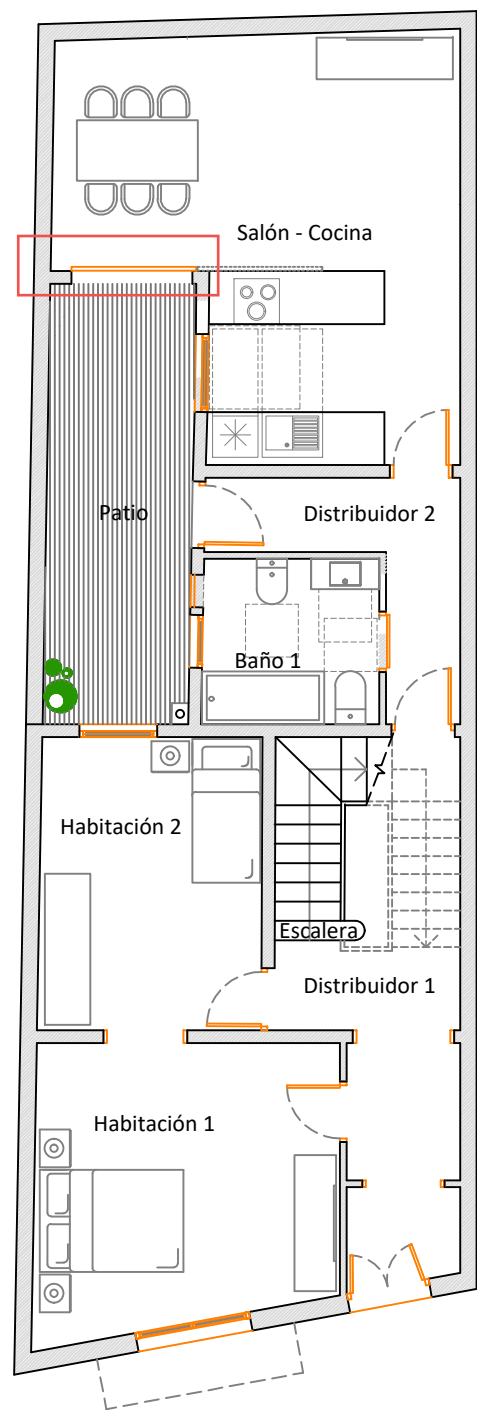


Planta baja

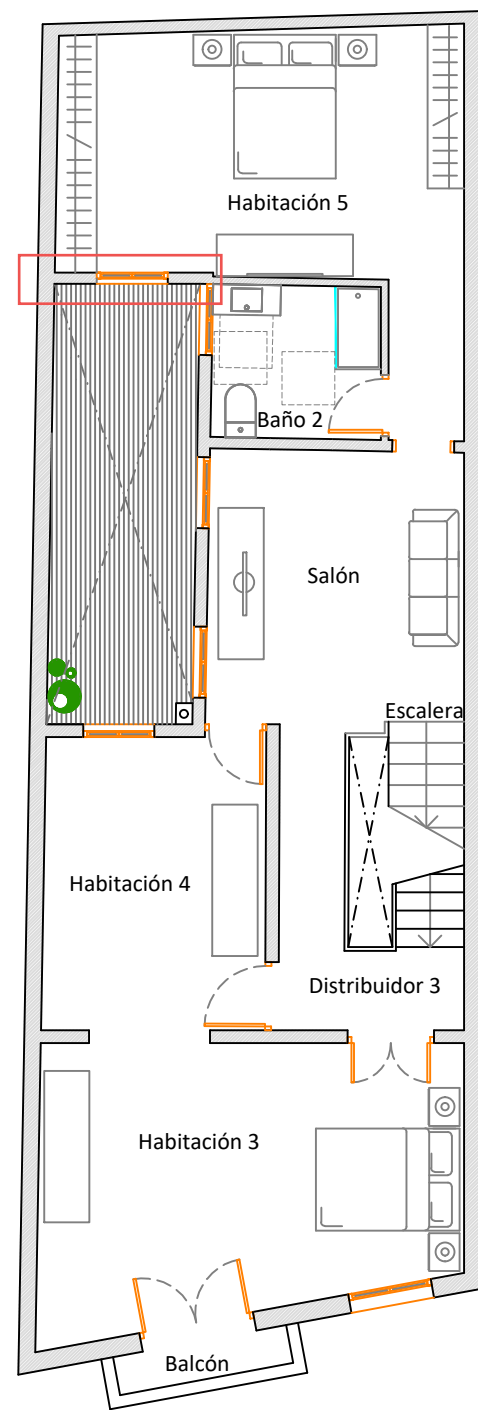

Planta alta

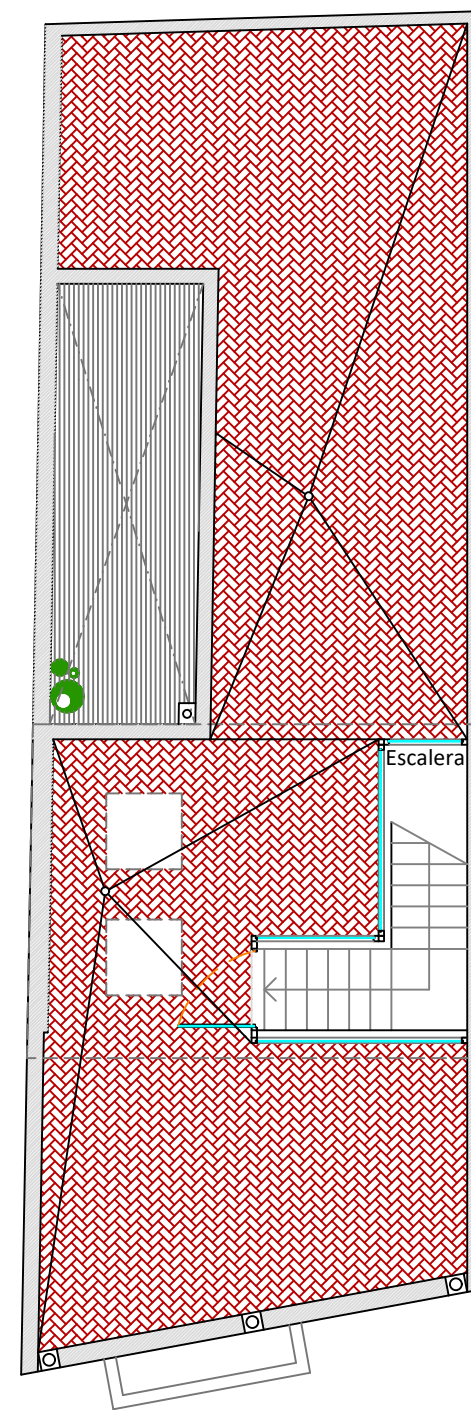

Planta cubierta

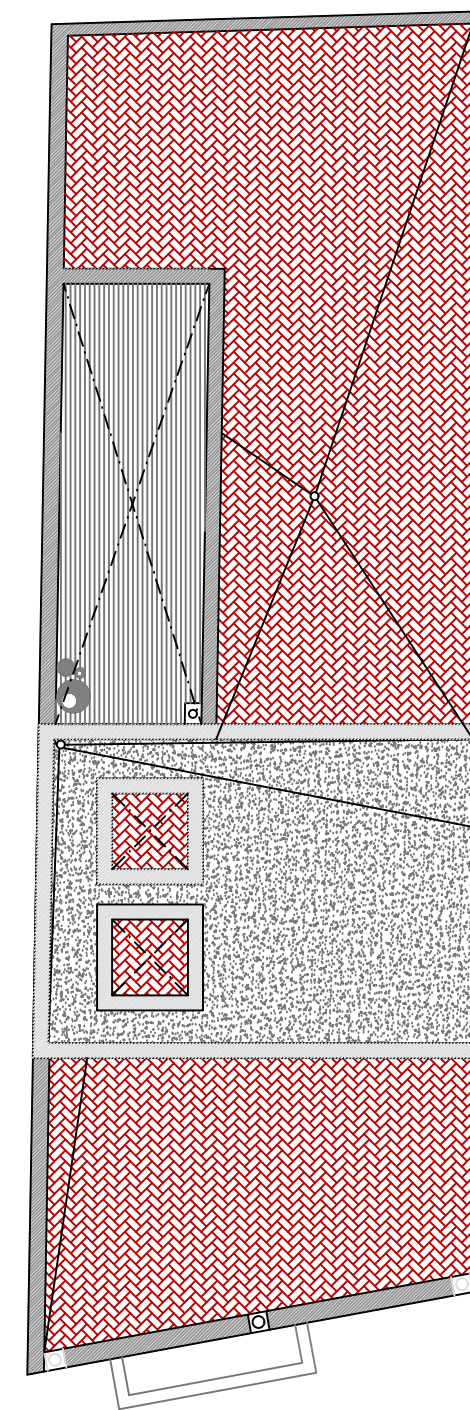

Planta sobrecubierta

PLANTA BAJA CUADRO DE SUPERFICIES		
	ÚTILES	CONSTRUIDA
HABITACIÓN 1	15.13 m ²	
HABITACIÓN 2	11.55 m ²	
DISTRIBUIDOR 1	11.53 m ²	
ESCALERA	3.09 m ²	
BAÑO 1	5.14 m ²	
DISTRIBUIDOR 2	5.79 m ²	
PATIO	11.37 m ²	
SALÓN - COCINA	25.54 m ²	
TOTAL ÚTIL	89.14 m ²	103.44 m ²

PLANTA ALTA CUADRO DE SUPERFICIES		
	ÚTILES	CONSTRUIDA
BALCÓN	1.37 m ²	
HABITACIÓN 3	20.49 m ²	
HABITACIÓN 4	10.47 m ²	
DISTRIBUIDOR 3	5.67 m ²	
ESCALERA	2.68 m ²	
SALÓN	12.3 m ²	
BAÑO 2	4.57 m ²	
HABITACIÓN 5	19.79 m ²	
TOTAL ÚTIL	77.34 m ²	103.44 m ²

PLANTA CUBIERTA CUADRO DE SUPERFICIES		
	ÚTILES	CONSTRUIDA
ESCALERA	5.58 m ²	
TOTAL ÚTIL	5.58 m ²	7.07 m ²

FERNANDO GARCIA ORTEGA

C/ Cruz verde, 21-23 3ª Planta Oficina O - 38003 Santa Cruz de Tenerife - telefono: 670 244 678 - fernando@calcularq.com

arquitecto

Demolición y reposición de forjado
y nuevo acceso a cubierta

Plantas estado reformado

plano nº

05

C/ San Miguel nº22 - CP:38002

escala

Septiembre 2016


sustituye

María Belén Lerena Guil - Alessandro Evangelista


propiedad




Sección A-A

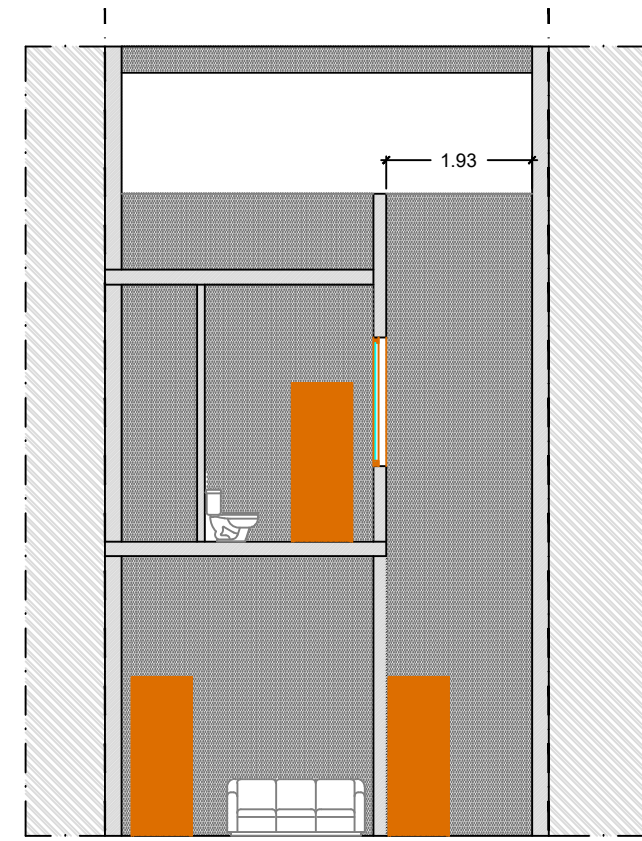

Sección C-C

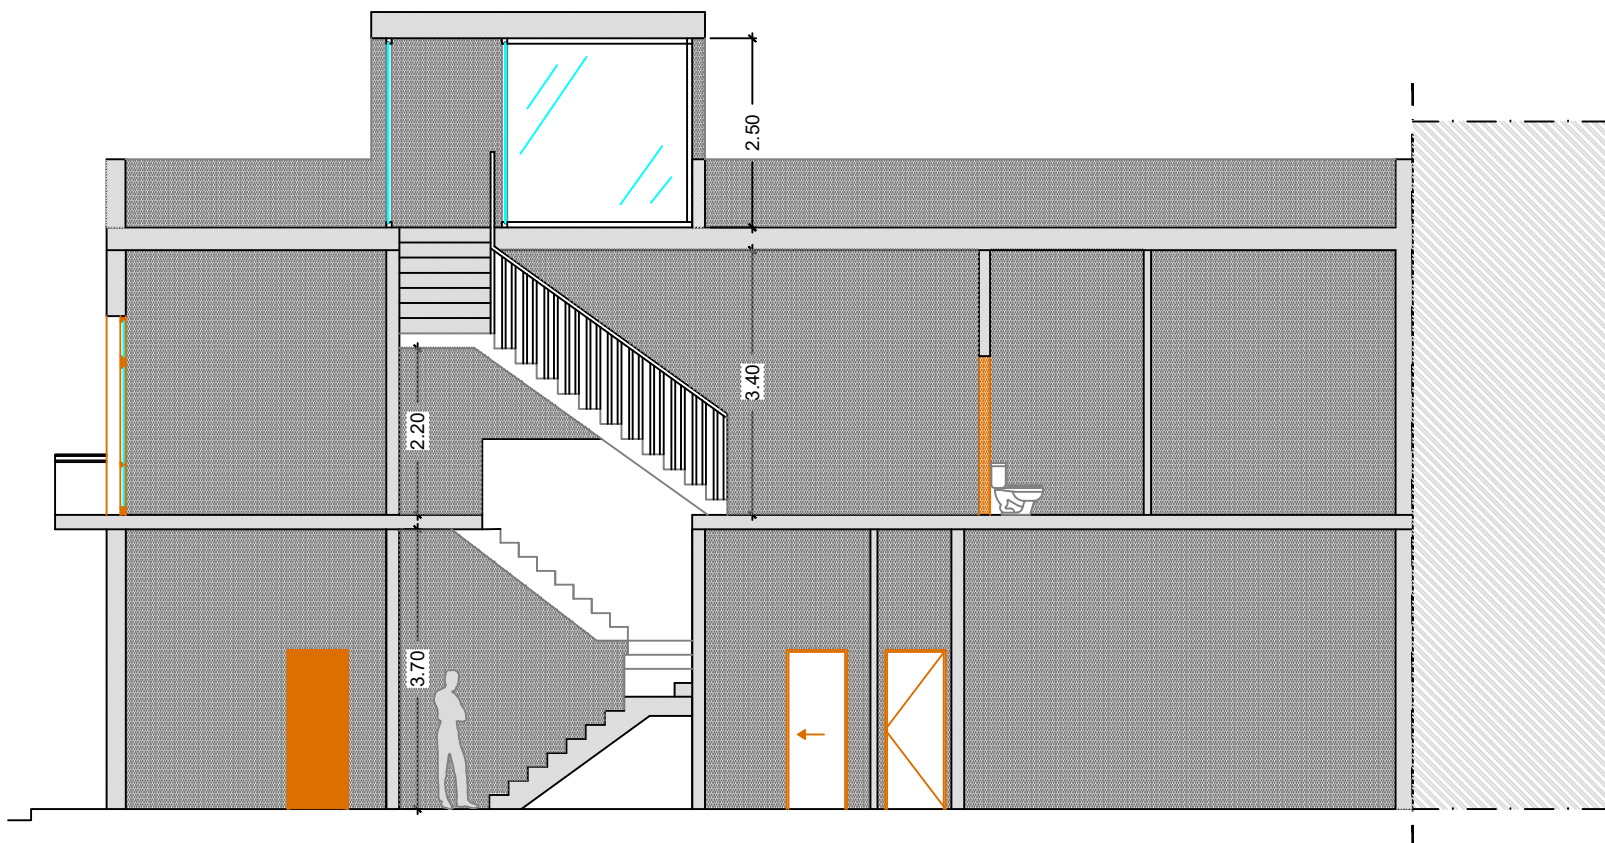


Sección B-B

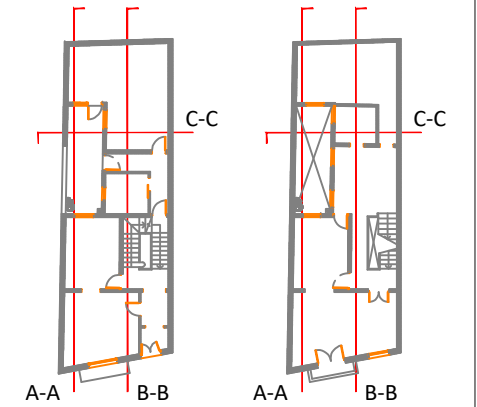


Planta
baja

Planta
alta

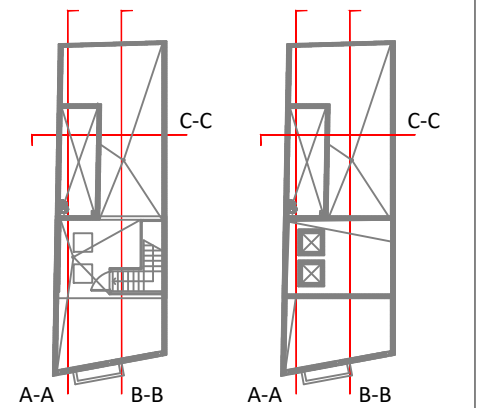

Planta
cubierta

Planta
sobrecubierta

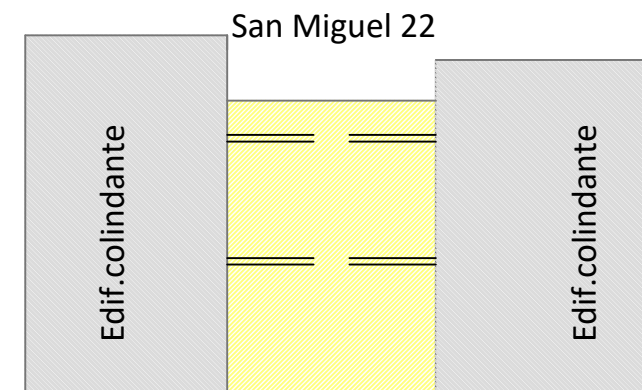

San Miguel 22

Volumetría estado reformado

FERNANDO GARCIA ORTEGA

C/ Cruz verde, 21-23 3ª Planta Oficina O - 38003 Santa Cruz de Tenerife - telefono: 670 244 678 - fernando@calcularq.com

arquitecto

Demolición y reposición de forjado y nuevo acceso a cubierta

Secciones estado reformado

plano nº

06

C/ San Miguel nº22 - CP:38002

escala

Septiembre 2016

sustituye


María Belén Lerena Guil - Alessandro Evangelista

propiedad


Límite edificación Área seccionada Edif.colindantes

ZONAS A DEMOLER


En negro: zonas ya demolidas o cuya demolición ya no es necesaria.

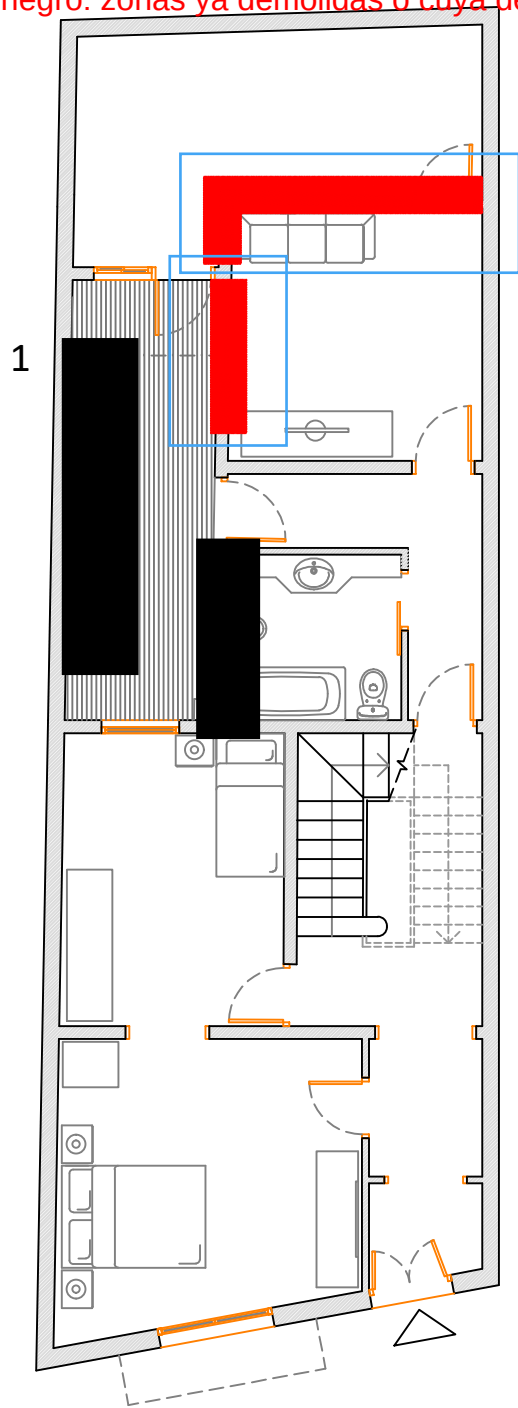


Planta baja

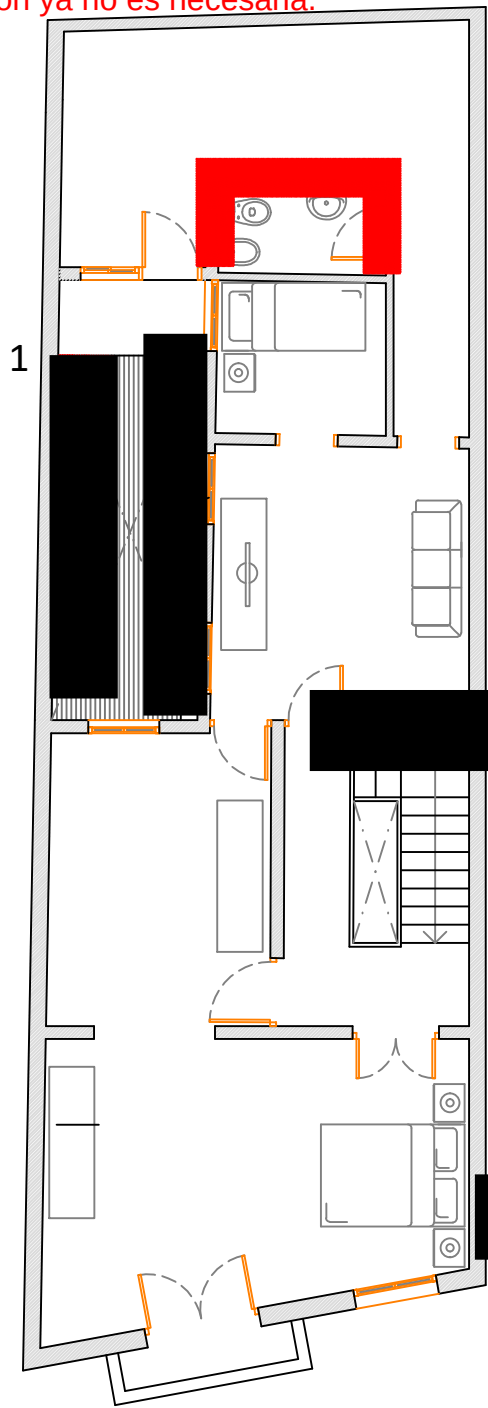


Planta alta

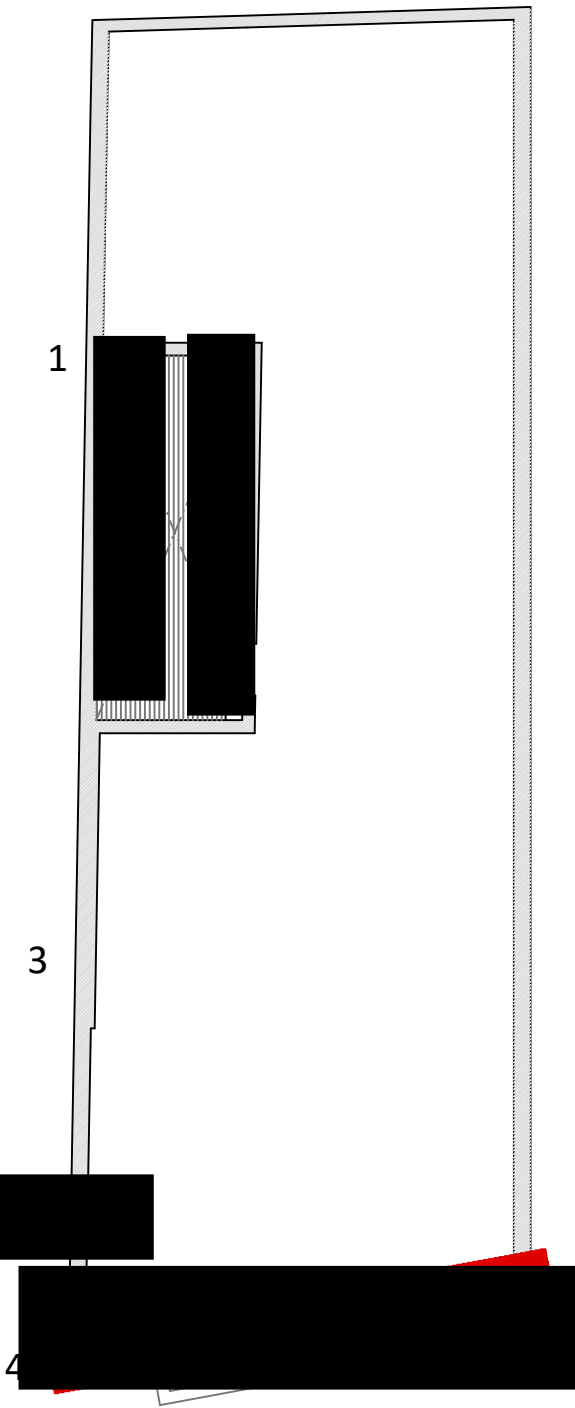


Planta cubierta

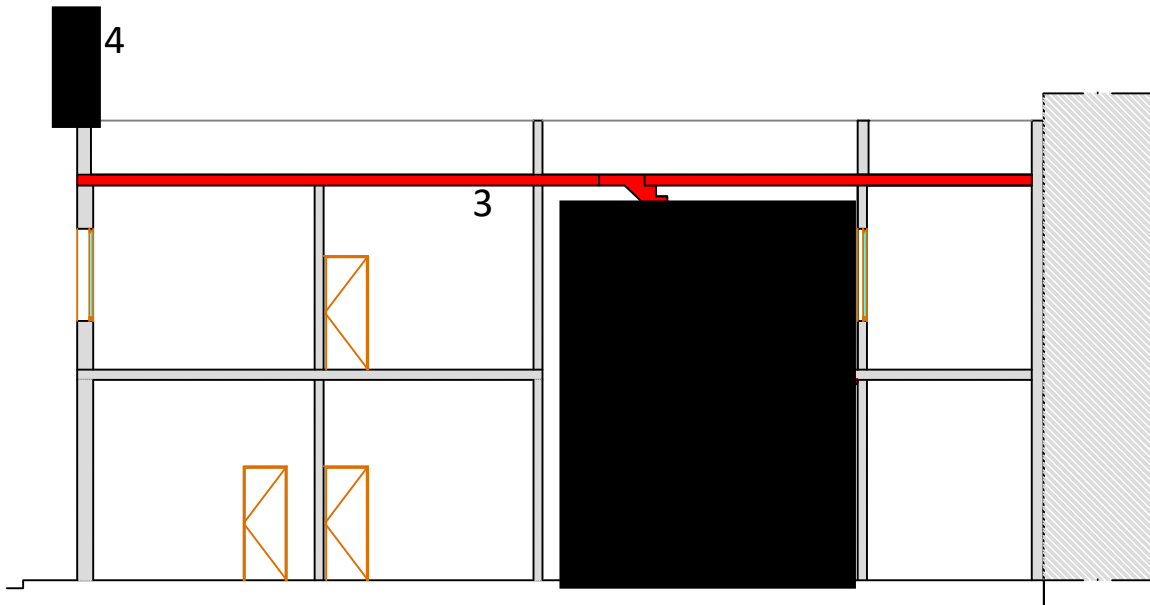


Sección A-A' estado actual con zonas a demoler

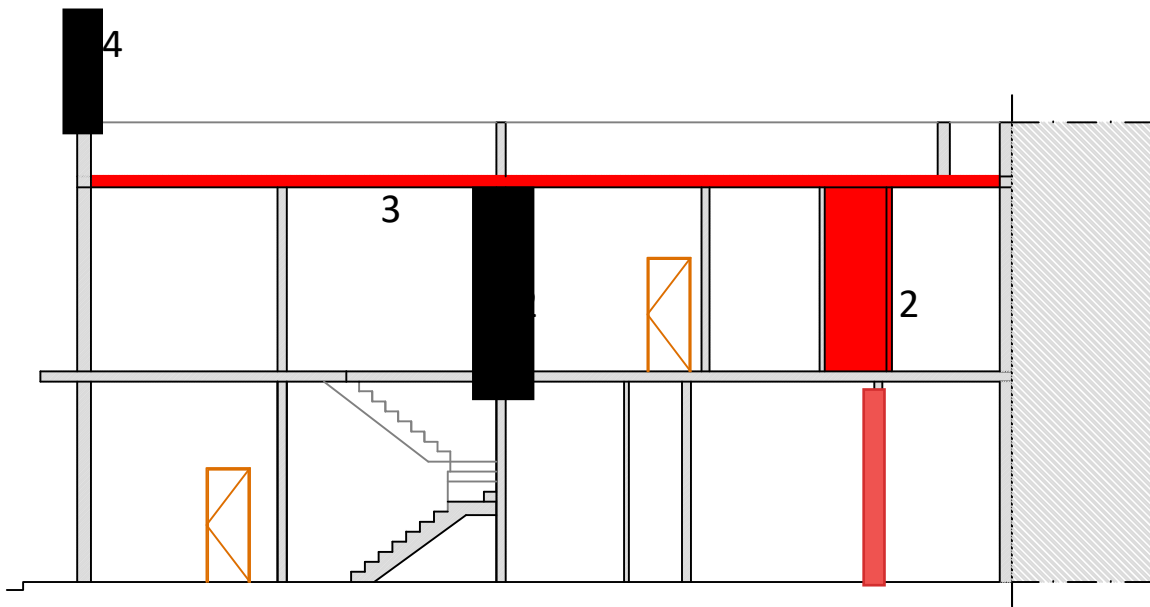

Sección B-B' estado actual con zonas a demoler

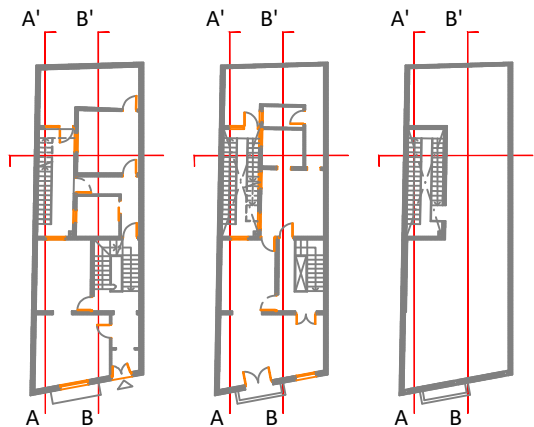

Estado actual

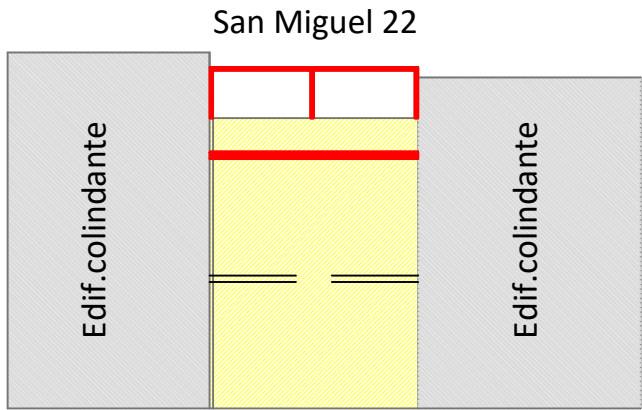

Volumetría existente

- Zonas a demoler
- 1.-

Losa escalera
- 2.-

Tabique
- 3.-

Forjado planta cubierta
- 4.-

Estructura de fachada

FERNANDO GARCIA ORTEGA

C/ Cruz verde, 21-23 3ª Planta Oficina O - 38003 Santa Cruz de Tenerife - telefono: 670 244 678 - fernando@calcularq.com

arquitecto

Demolición y reposición de forjado y nuevo acceso a cubierta

Zonas a demoler

plano nº

07

C/ San Miguel nº22 - CP:38002

escala

Septiembre 2016

sustituye

María Belén Lerena Guil - Alessandro Evangelista

propiedad





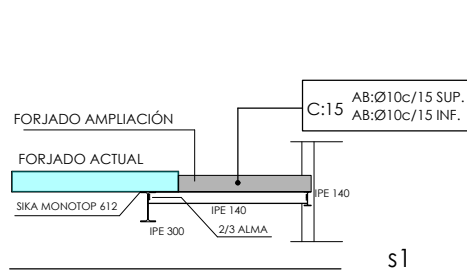


Tabla de vigas centradoras	
VC.T-1	Arm. sup.: 4Ø16
	Arm. inf.: 3Ø12
	Arm. piel: 1x2Ø12
	Estribos: 1xØ8c/30

CUADRO DE ELEMENTOS DE CIMENTACIÓN						
Referencias	Dimensiones (cm)	Canto (cm)	Armado inf. X	Armado inf. Y	Armado sup. X	Armado sup. Y
P1	45x85	50	4Ø12c/21	2Ø12c/25		
P2	85x85	50	4Ø12c/21	4Ø12c/21		
P4	105x105	50	5Ø12c/21	5Ø12c/21		
P8	55x105	50	5Ø12c/21	3Ø12c/17		
P5-P7	170x45	50	2Ø12c/25	7Ø12c/25	2Ø12c/25	7Ø12c/25
P6-P3	190x55	50	3Ø12c/17	8Ø12c/24		

P3	P4	P5	P6	P7	SOBRECUBIERTAS
H	I	H			
HEB-120	HEB-120	HEB-120			
H	I	H	H	H	PRIMERA
HEB-120	HEB-120	HEB-120	HEB-120	HEB-120	
					Cimentación

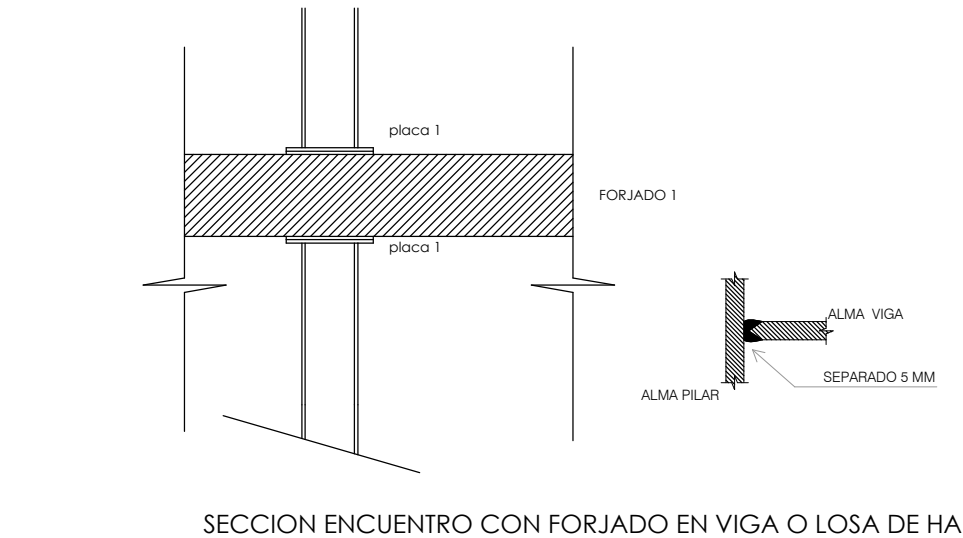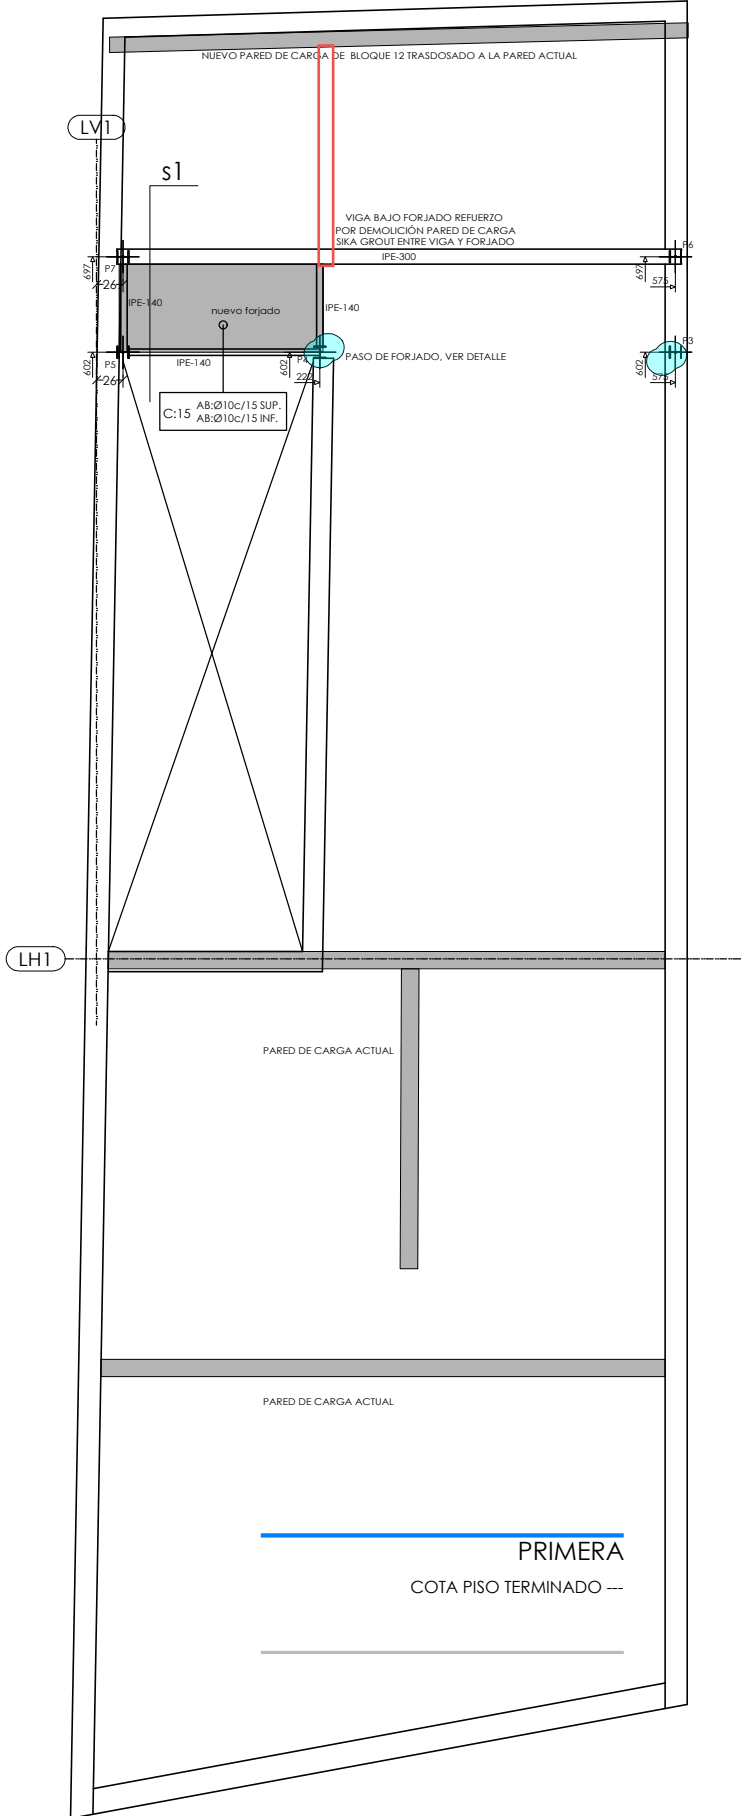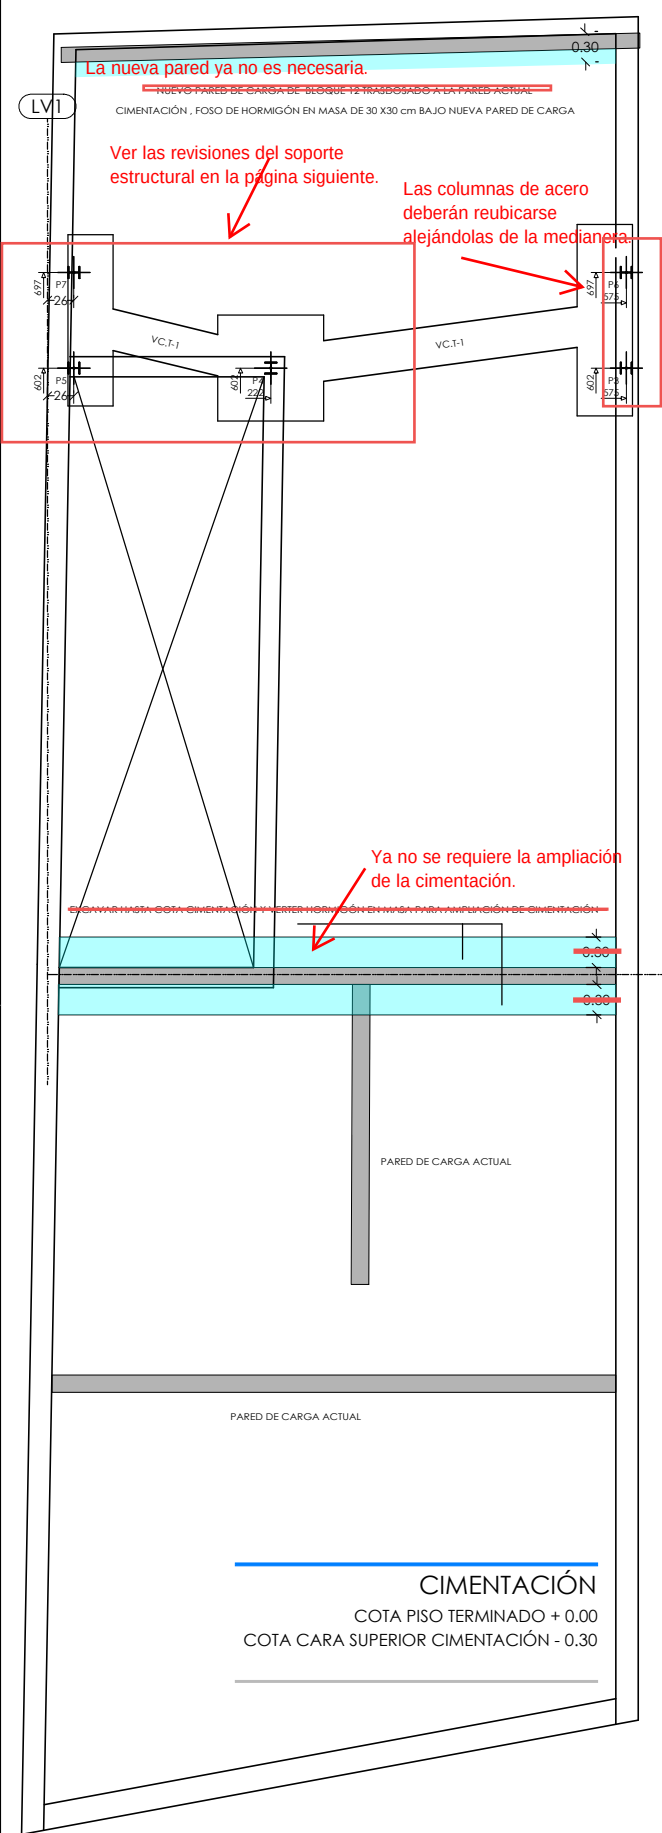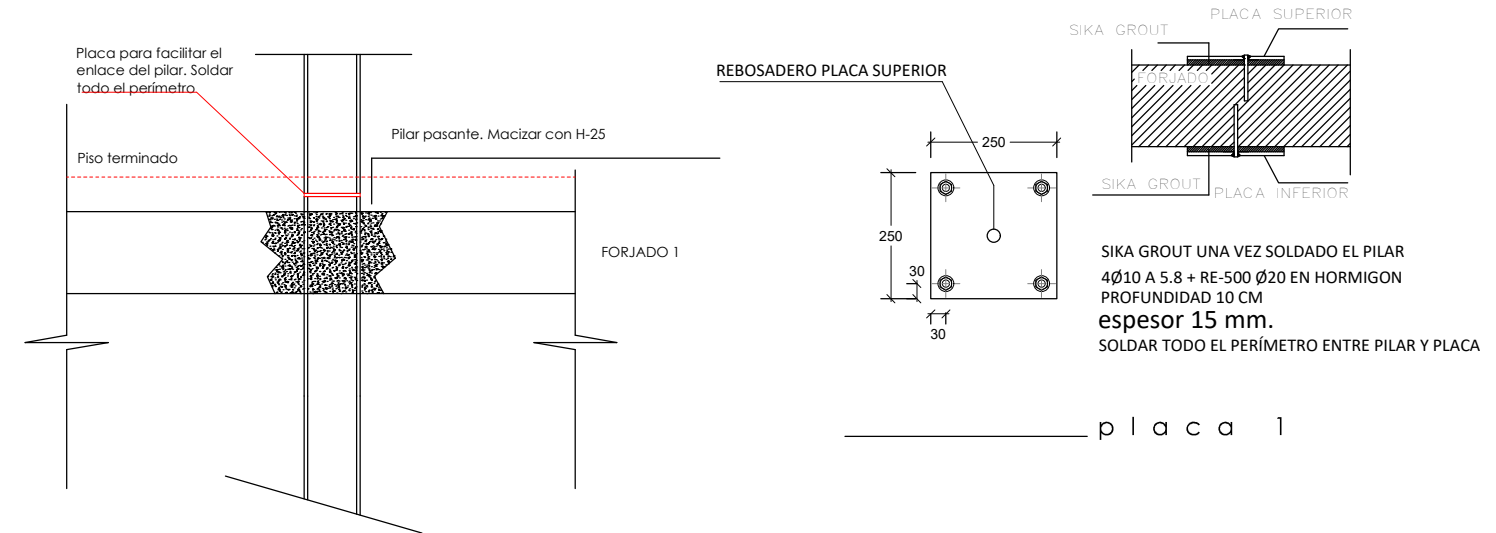

SECCION ENCUESTRO CON FORJADO. BOVEDILLAS

GARCIA ORTEGA FERNANDO - 42178098P

Firmado digitalmente por GARCIA ORTEGA FERNANDO - 42178098P
Nombre de reconocimiento (DN): c=ES, serialNumber=IDCES-42178098P, givenName=FERNANDO, sn=GARCIA ORTEGA, cn=GARCIA ORTEGA FERNANDO - 42178098P
Fecha: 2026.07.09 20:29:22 +01'00'

FERNANDO GARCIA ORTEGA
C/ Cruz verde, 21-23 3ª Planta Oficina O - 38003 Santa Cruz de Tenerife - telefono: 670 244 678 - fernando@calcularq.com

arquitecto

Demolición y reposición de forjado y nuevo acceso a cubierta

CIMENTACIÓN
REFUERZO PRIMER FORJADO

C/ San Miguel nº22 - CP:38002

escala 1/75

Septiembre 2016


sustituye

María Belén Lerena Guil - Alessandro Evangelista

propiedad

plano nº

V1_1

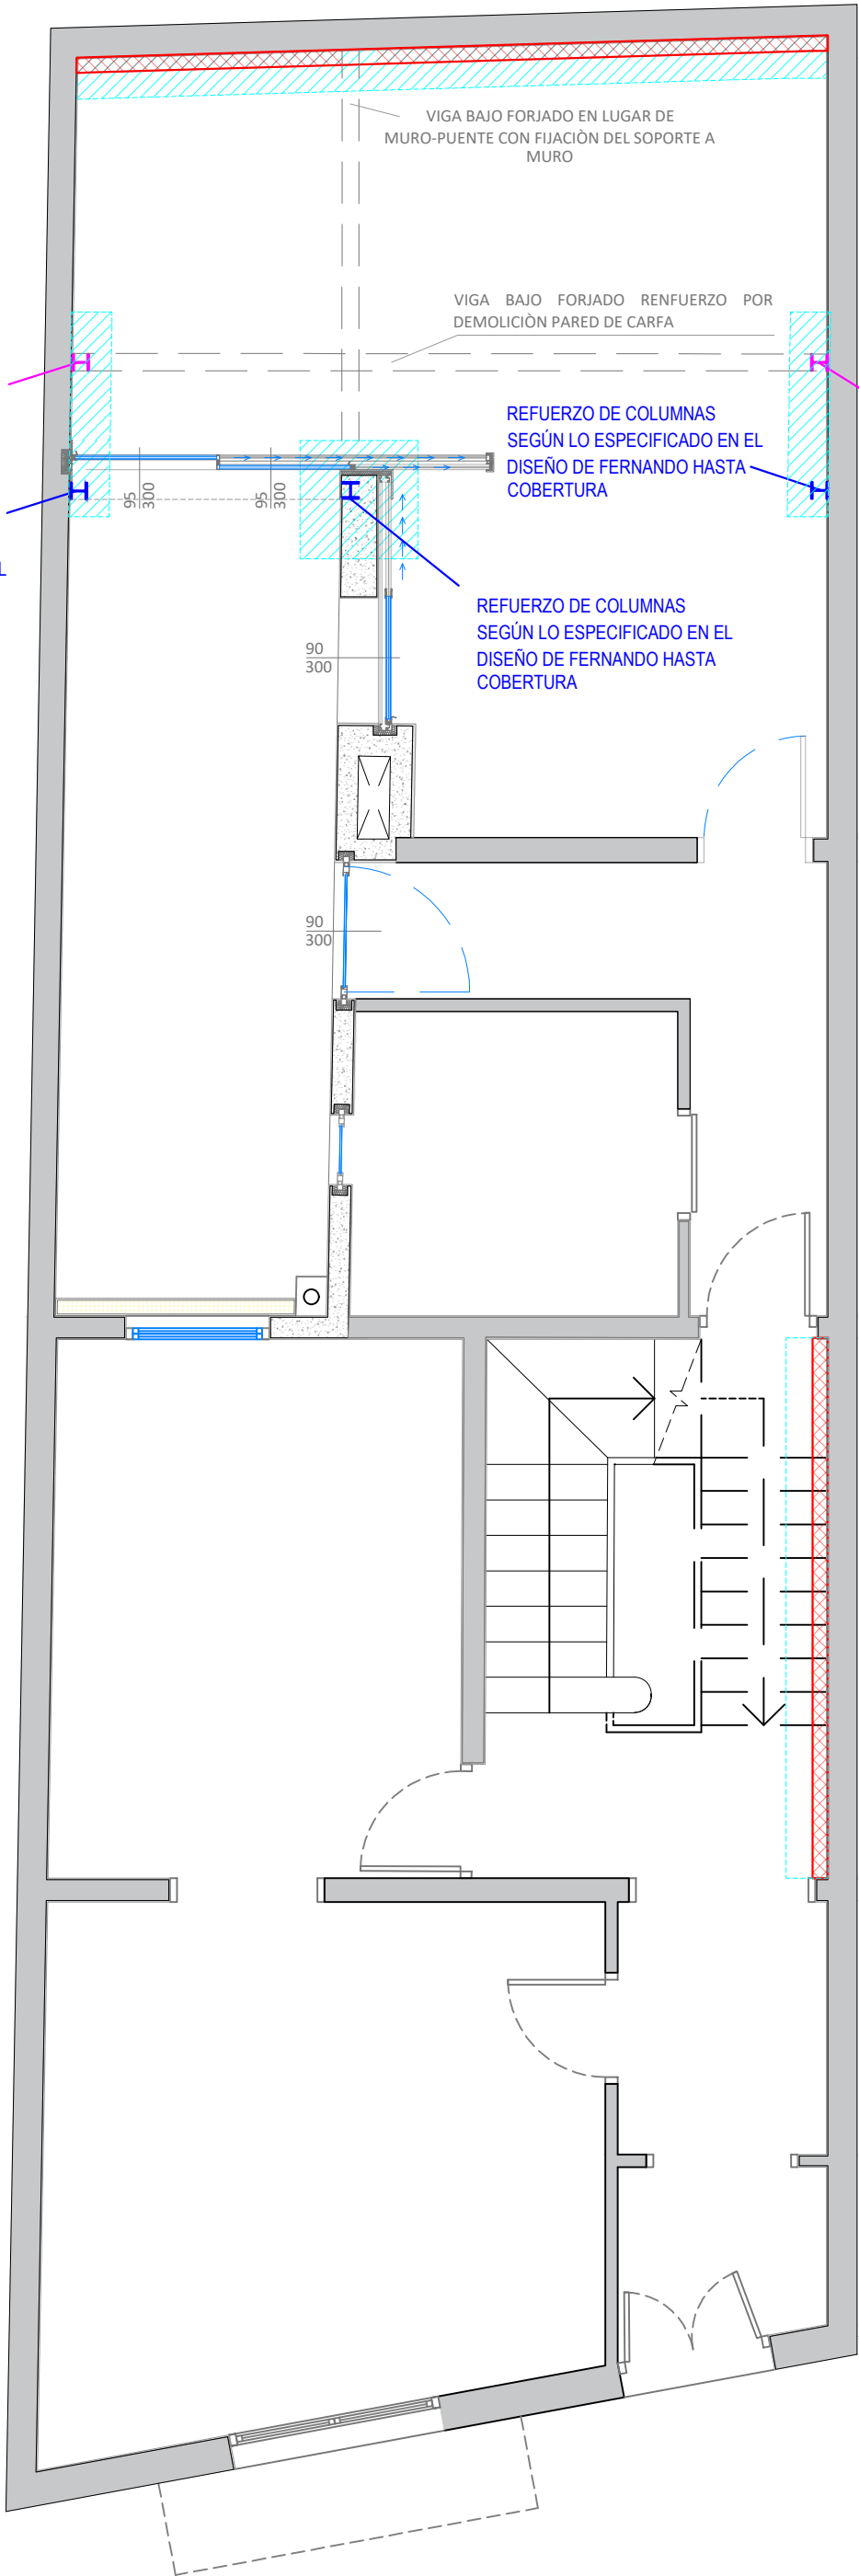

REFUERZO DE COLUMNAS
SEGÚN LO ESPECIFICADO EN
EL DISEÑO DE FERNANDO
HASTA FORJADO NIVEL 1

REFUERZO DE COLUMNAS
SEGÚN LO ESPECIFICADO EN EL
DISEÑO DE FERNANDO HASTA
COBERTURA

REFUERZO DE COLUMNAS
SEGÚN LO ESPECIFICADO EN EL
DISEÑO DE FERNANDO HASTA
COBERTURA

REFUERZO DE COLUMNAS
SEGÚN LO ESPECIFICADO EN EL
DISEÑO DE FERNANDO HASTA
COBERTURA

REFUERZO DE COLUMNAS
SEGÚN LO ESPECIFICADO EN
EL DISEÑO DE FERNANDO
HASTA FORJADO NIVEL 1

VIGA BAJO FORJADO EN LUGAR DE
MURO-PUENTE CON FIJACIÓN DEL SOPORTE A
MURO


VIGA BAJO FORJADO RENFUERZO POR
DEMOLICIÓN PARED DE CARFA

-  nueva pared de carga
muro en bloques macizos
-  cimentacion bajotierra

PLANTA BAJA

ESCALA 1:50

El diseño de la abertura del forjado de cubierta para la escalera deberá modificarse para rellenar las zonas resaltadas en amarillo.

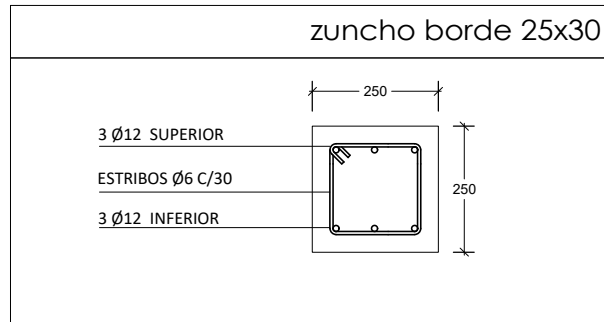

CUADRO DE CARACTERÍSTICAS DE FORJADO

Características del forjado

Canto del forjado: 25x5 cm.
Viguetas semienterentes
con la armadura siguiente:
según dimensionamiento cálculo
Armadura Negativos: mallazo de reparto
25x25#6

Enlace de nervios con apoyo.

Tabla de características de forjados de viguetas (Grupo 1)

FORJADO DE VIGUETAS DE HORMIGÓN

Canto de bovedilla: 25 cm
Espesor capa compresión: 5 cm
Inteireje: 72 cm
Bovedilla: POLIESTIRENO
Ancho del nervio: 12 cm
Volumen de hormigón: 0.088 m³/m²
Peso propio: 2.25 kN/m²
Nota: Consulte los detalles referentes a enlaces con forjados de la estructura principal y de las zonas macizadas.

Viga plana en Extremo de vano

VIGA PLANA EN EXTREMO Y CENTRO DE VANO. VIGUETAS PARALELAS.



EXTREMO DE VANO SOBRE VIGA DE CANTO DESCOLGADA
VIGUETAS DE CELOSIA

arquitecto



plano nº **V1 2**

propiedad

escala 1/75








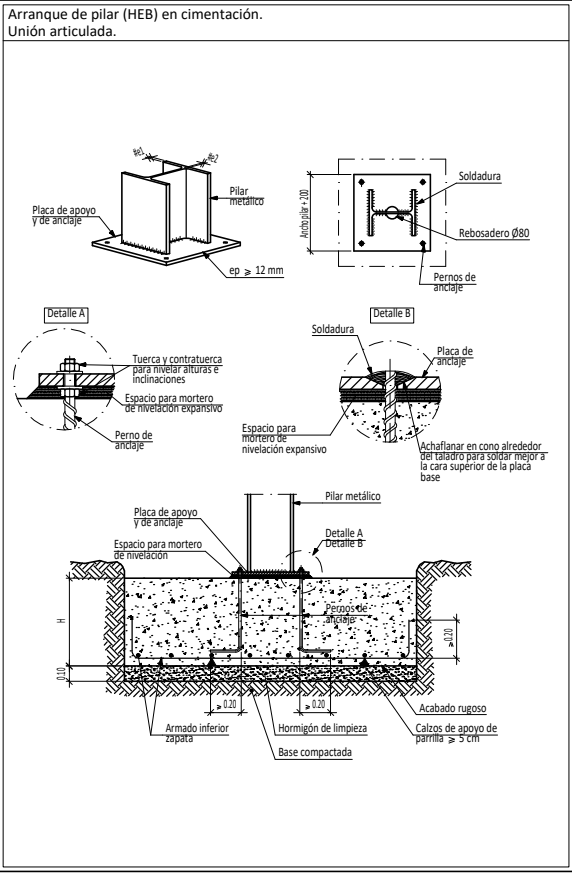
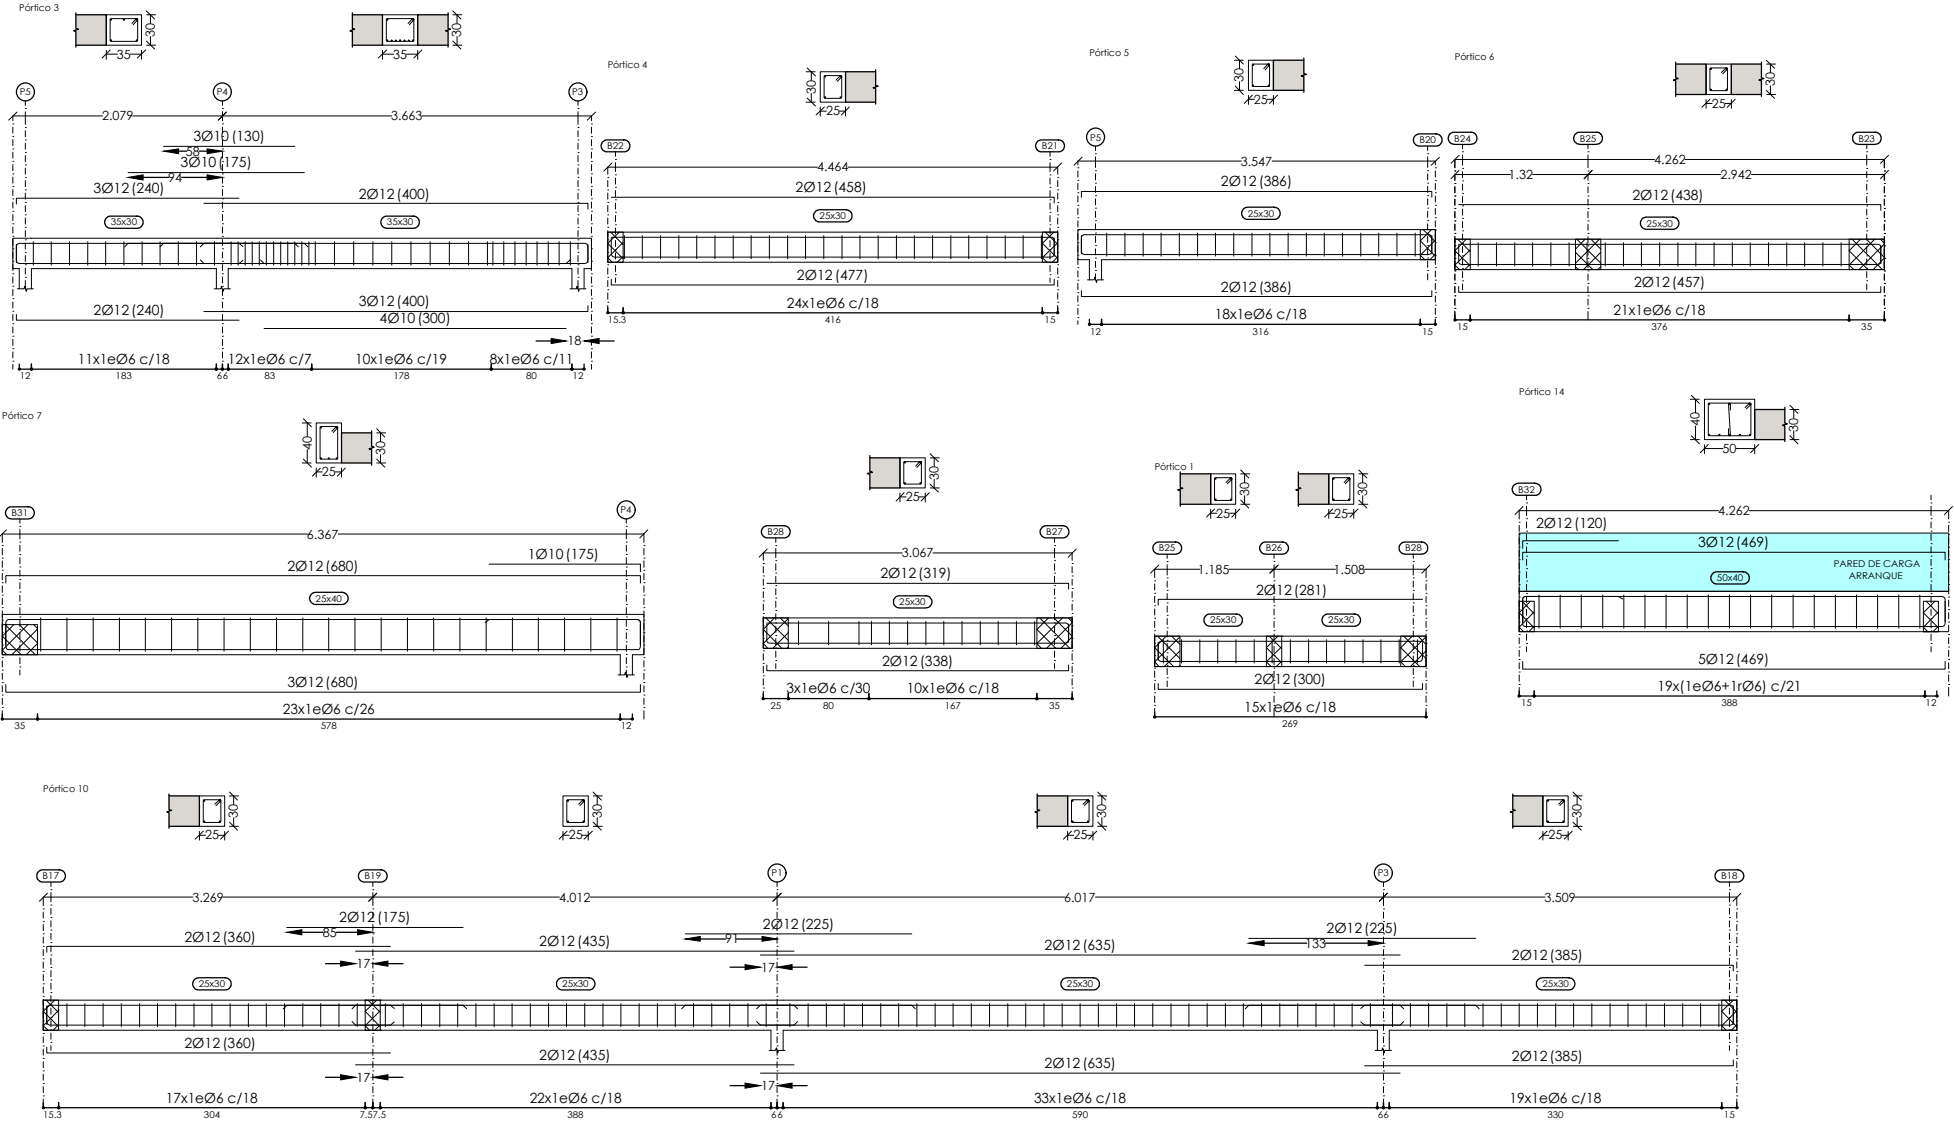


SEGUNDA

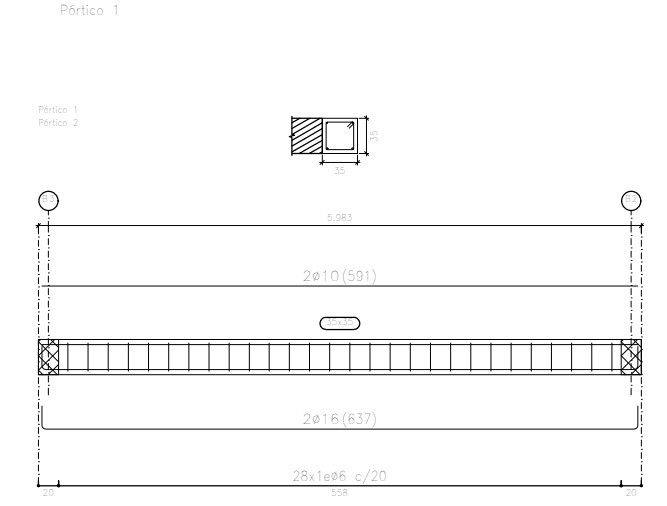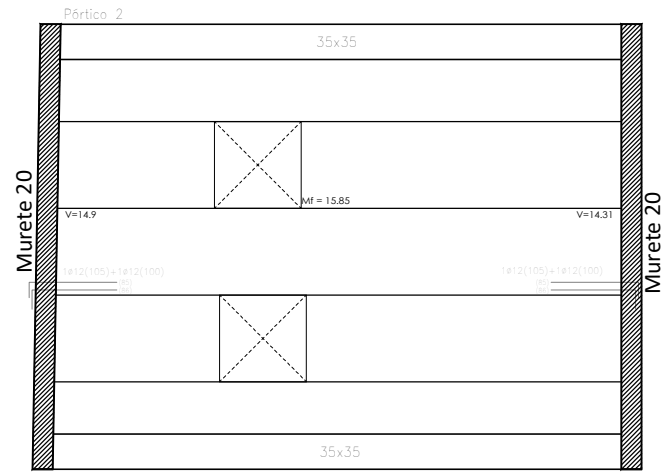


SOBRECUBIERTAS
H LIBRE DESDE PISO TERMINADO 2.50


Este plano se complementa con el de detalles generales y los de albañilería en cuanto a características de la estructura, replanteo de pilares, vuelos, huecos, instalaciones, etc.							
ELEMENTO		LOCALIZACIÓN					
		PILARES		LOSAS Y FORJADOS	CIMENTACION		
DESIGNACIÓN (Art. 39)		HA-25/620/Ita	HA-25/620/Ita	HA-25/620/Ita	HA-25/620/Ita		
Resistencia característica f _{cd} (N/mm ²)	a 7 días	20	20	20	20		
	a 28 días	25	25	25	25		
CONSISTENCIA (Art. 30.6.1)		BLANDA	BLANDA	BLANDA	BLANDA		
ASENTO COMO ABRAS (cm)		6-9	6-9	6-9	6-9		
ARIDO (Art.28.2)	Tipos	RODADO	RODADO	RODADO	RODADO		
	Tamaño máximo(mm)	20	20	20	20		
Ambiente (art.8.2.1.1)		Ia Interiores sometidos a humedad alta			r<35mm. normal		
CEMENTO (Art.26)		CEM-III/A-V 42.5-R					
TIPO Y CLASE							
COEFICIENTE DE MINORACION	E _{ci}	Comb. Acc.	Comb. Acc.	Comb. Acc.	Comb. Acc.		
		1,5	1,3	1,5	1,3	1,5	1,3
DESIGNACIÓN		B500S	B500S	B500S	B500S		
LÍMITE ELÁSTICO f _{yk} (N/mm ²)		500	500	500	500		
COEFICIENTE DE MINORACION	E _{st}	1,15	1,15	1,15	1,15		
μ=2							
CONTROL DE EJECUCIÓN		ESTADÍSTICO (Art. 31)		SOBRECARGAS		CONCARGAS	
COEFICIENTE DE MAYORACION DE CARGAS				E _{fi} 1,6		E _{fi} 1,5	
CARGAS GRAVITATORIAS APLICADAS EN LA OBRA							
FORJADO TIPO		SOBRECARGAS			CONCARGAS		
		PESO PROPIO					
		USO PRIVADO	USO PÚBLICO	NEVE	SOLERA/CUBRIMIENTO	PRETI/CERRAMIENTO	
FORJADO CUBIERTA NO-TRANSITABLE		1 kN/m2	-	0.2 kN/m2	2 kN/m2	4 kN/m2	2.25 kN/m2
FORJADO CUBIERTA TRANSITABLE		2 kN/m2	-	0.2 kN/m2	2 Kjn/m2	4 kN/m2	2.25 kN/m2

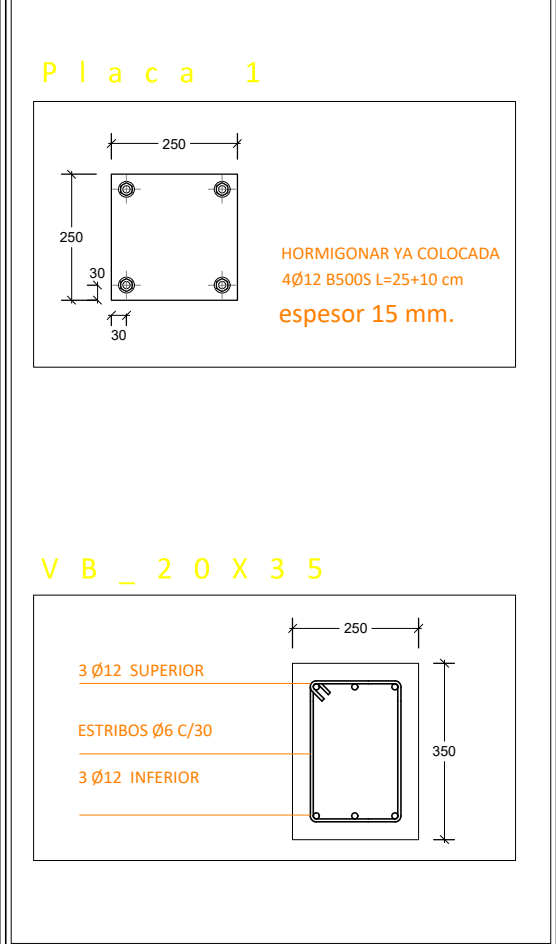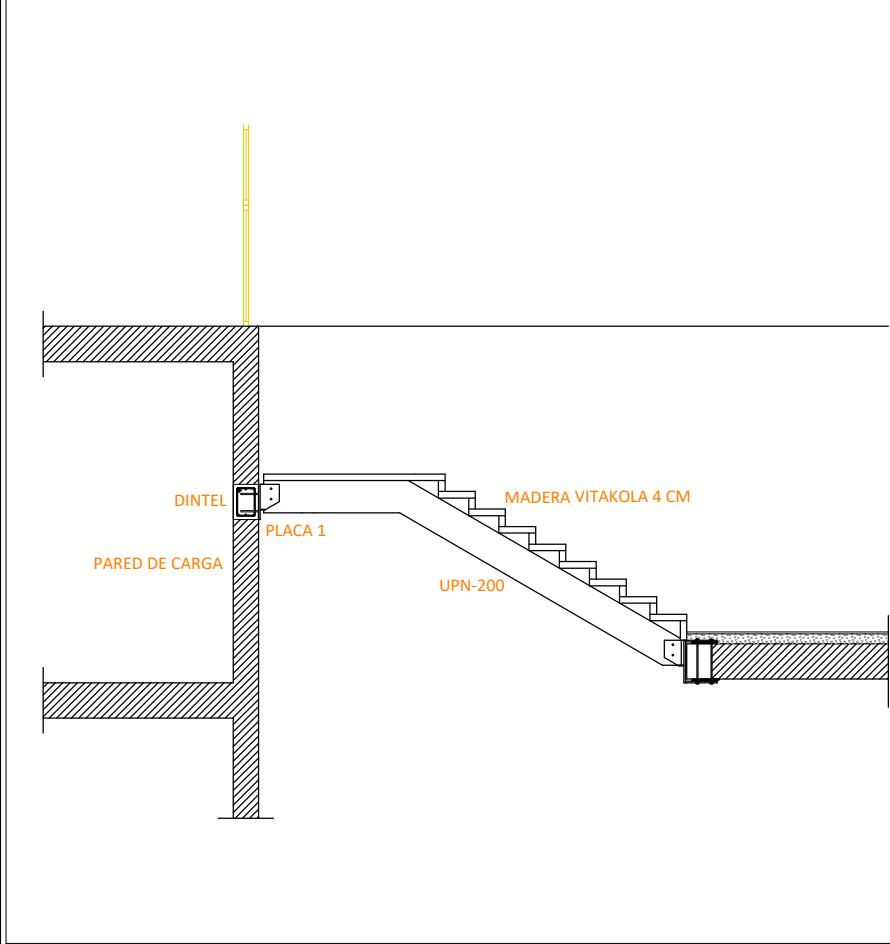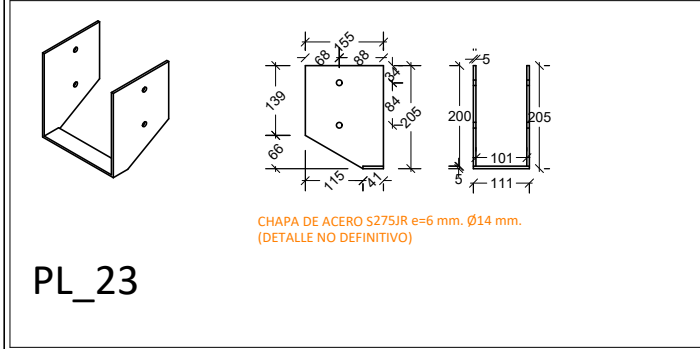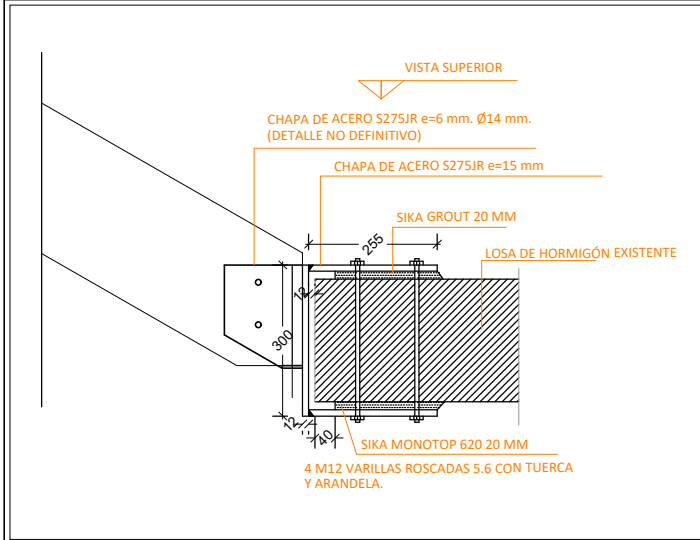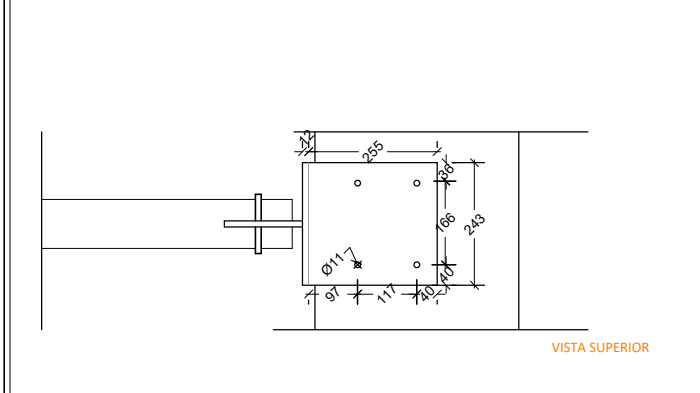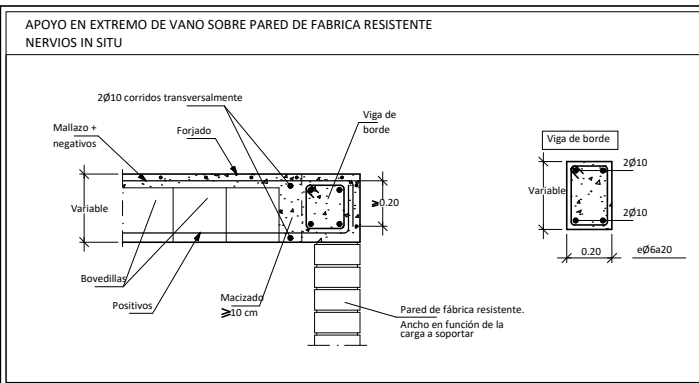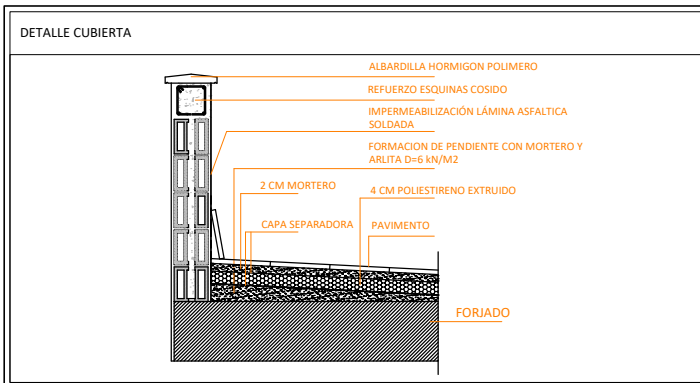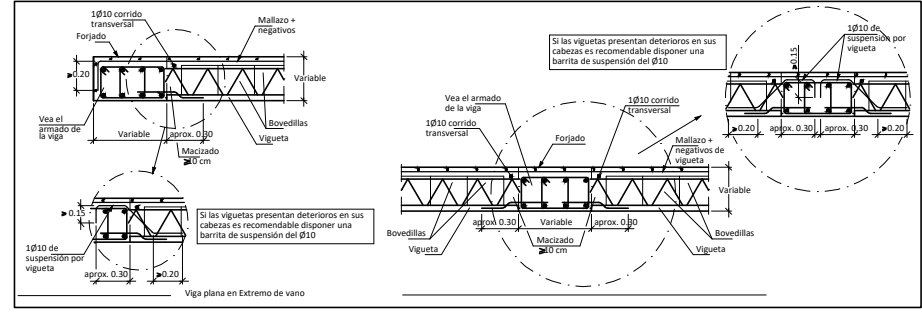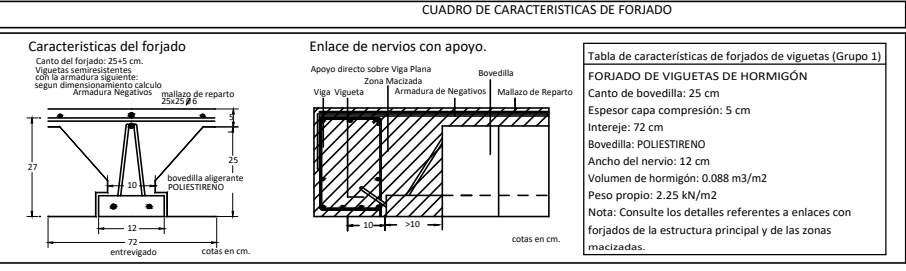


El drenaje de la terraza deberá modificarse de acuerdo con el plano de la página siguiente.

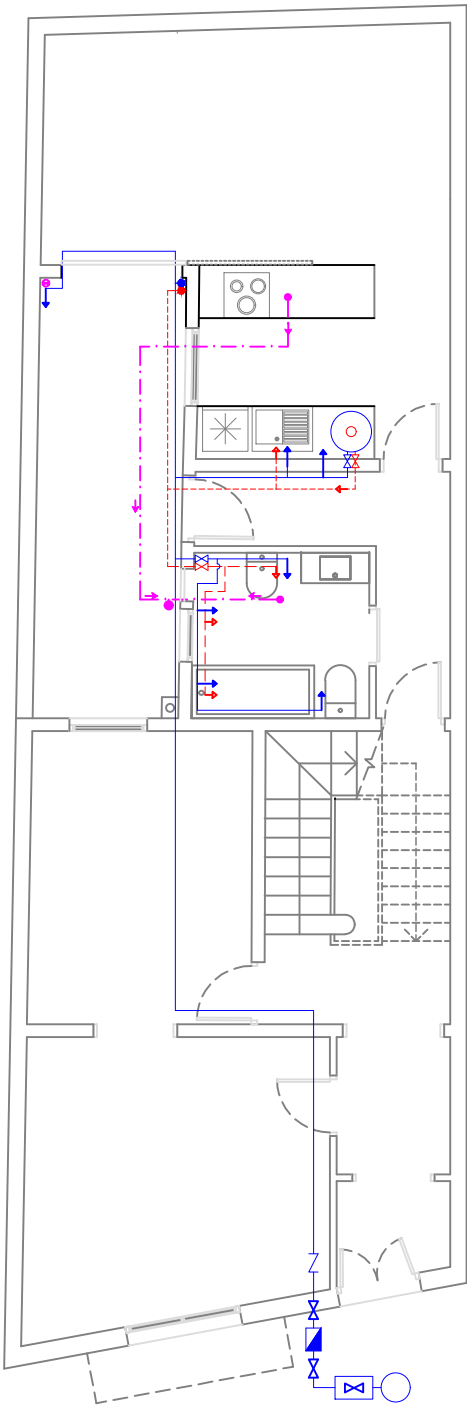


Planta baja

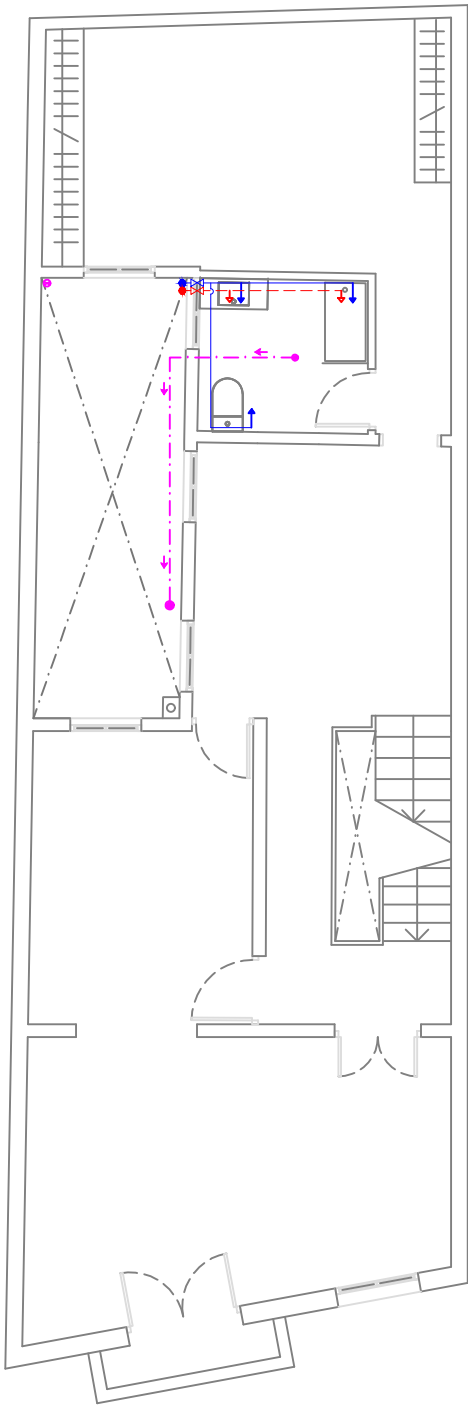

Planta alta

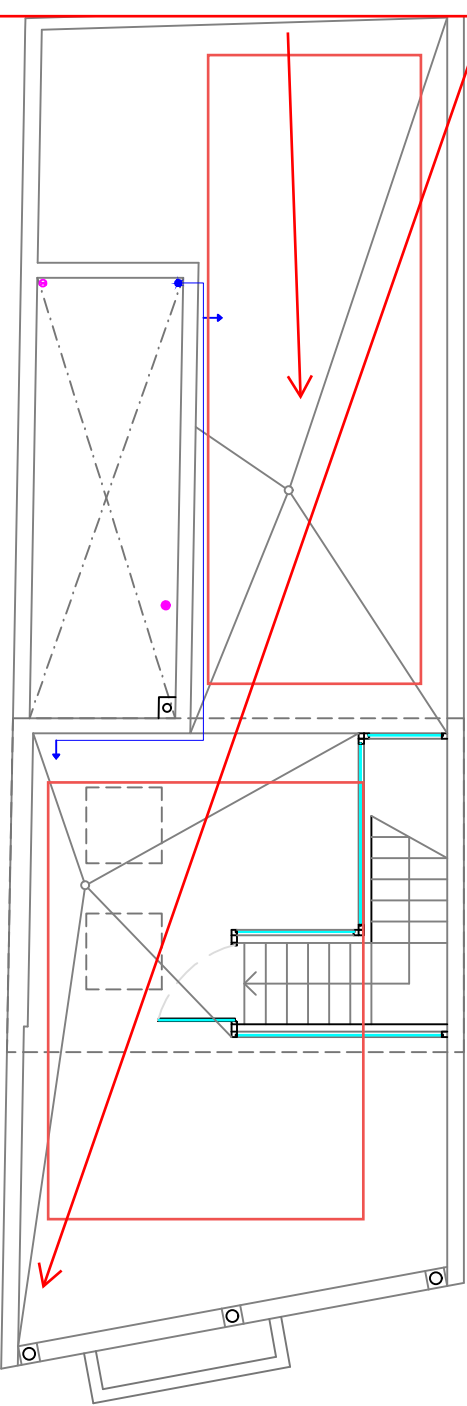

Planta cubierta

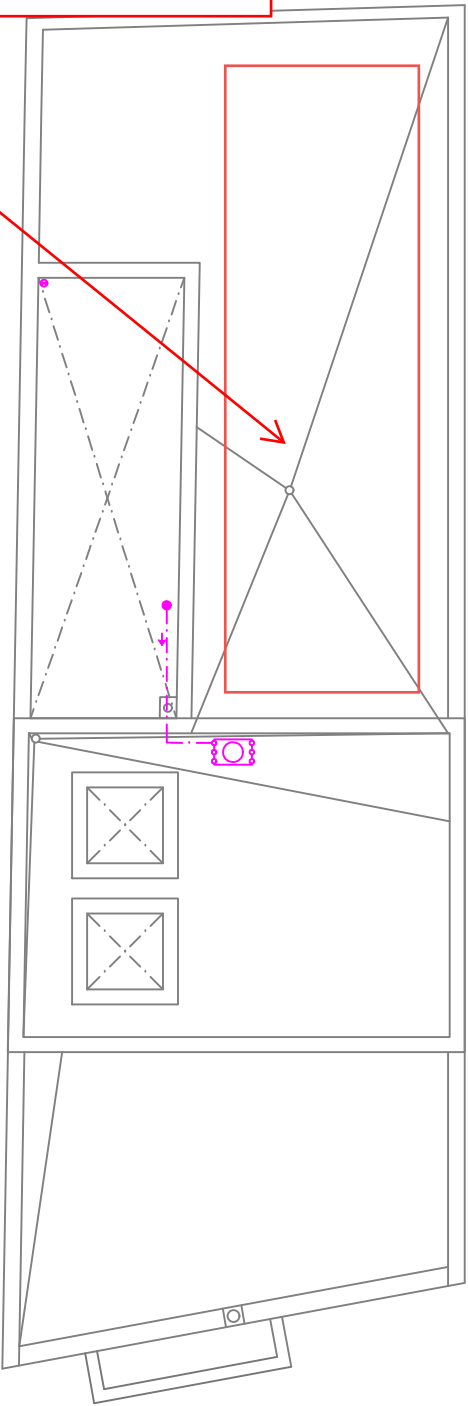

Planta sobrecubierta

Conducto horizontal de extracción de aire mecánica	
Tubería agua fría	
Lave de corte general	
Contador general	
Llave antiretorno	
Lave de corte	

Conducto vertical de extracción de aire mecánica	
Tubería agua caliente	
Punto de agua fría	
Punto de agua caliente	
Tubería ascendente agua fría	
Tubería ascendente agua caliente	

Conducto vertical de extracción de vapores y contaminantes de cocción	
Apertura de admisión de extracción de aire mecánica	
Aspirador mecánico para extracción de aire	
Termo	
Acometida	

FERNANDO GARCIA ORTEGA

C/ Cruz verde, 21-23 3ª Planta Oficina O - 38003 Santa Cruz de Tenerife - telefono: 670 244 678 - fernando@calcularq.com

arquitecto

Demolición y reposición de forjado y nuevo acceso a cubierta

Fontanería y Ventilación estado reformado

plano nº 14


C/ San Miguel nº22 - CP:38002


escala Septiembre 2016

sustituye


María Belén Lerena Guil - Alessandro Evangelista

propiedad


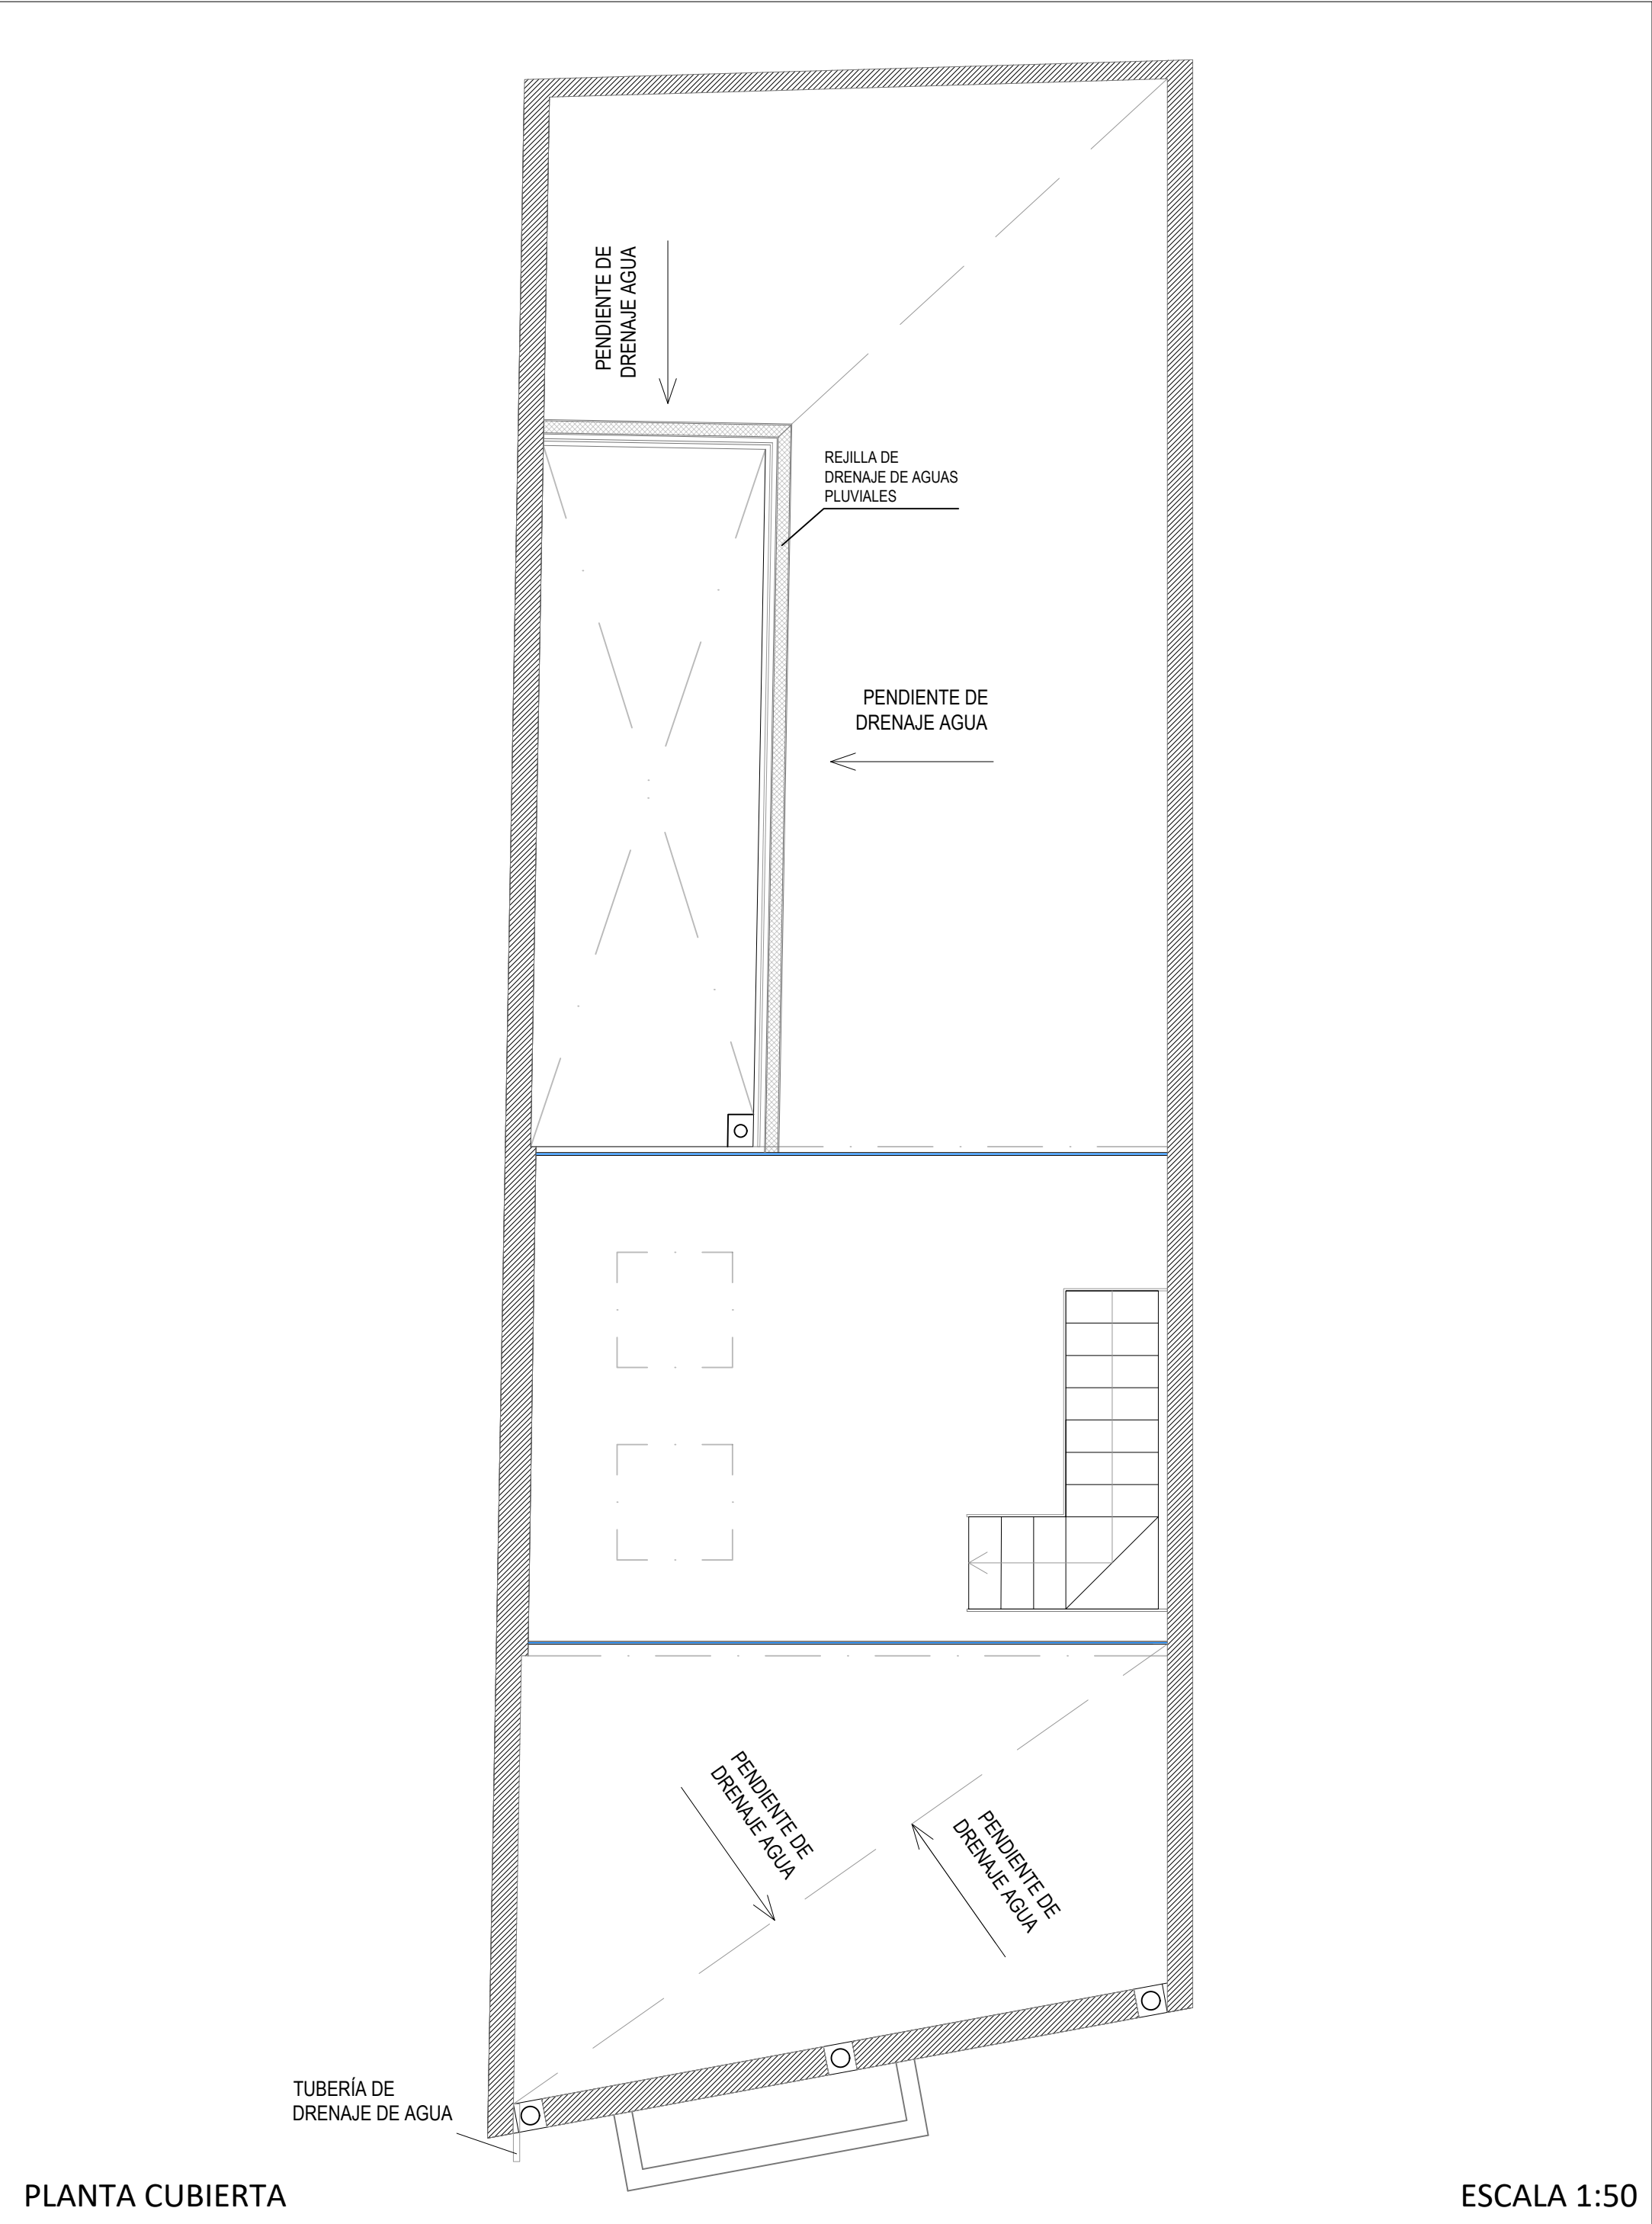


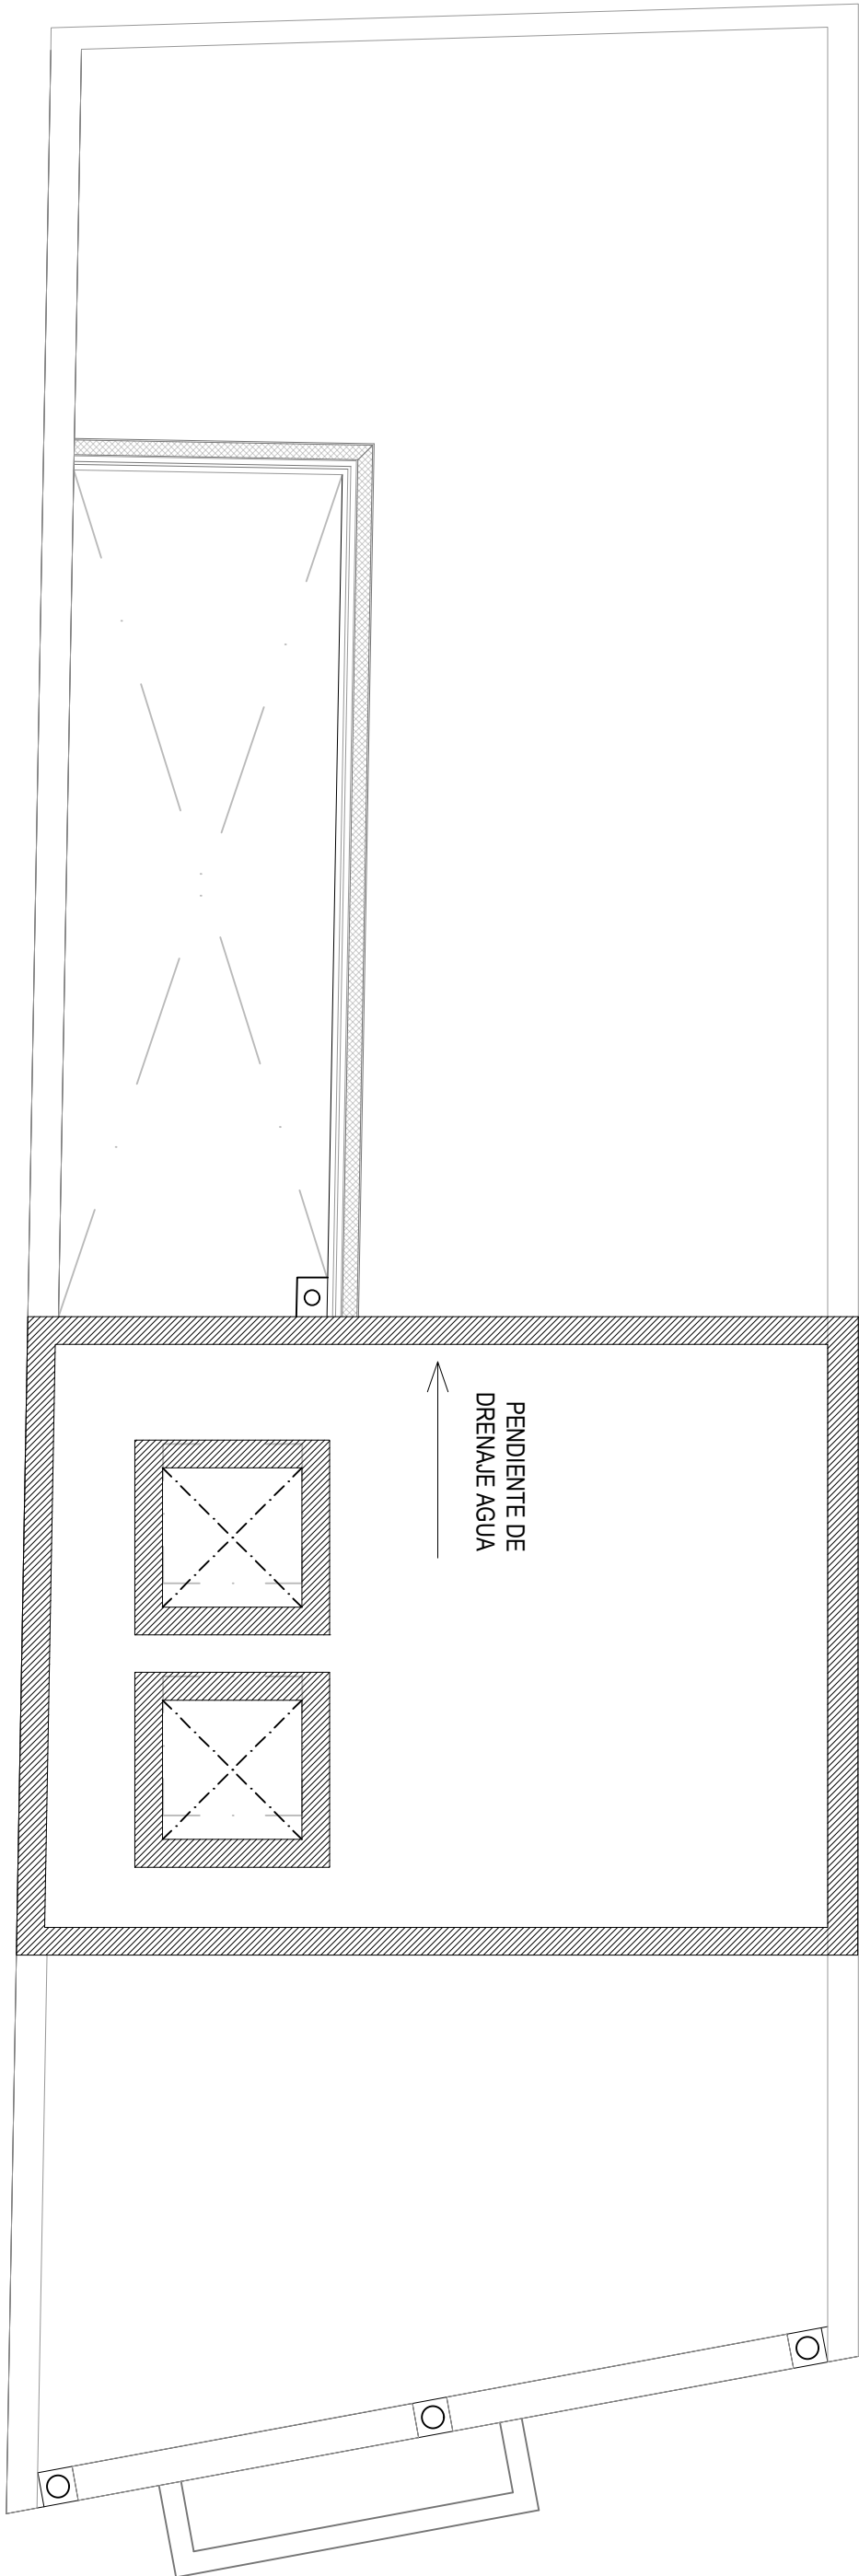


Modificaciones de las aberturas de las ventanas del patio.

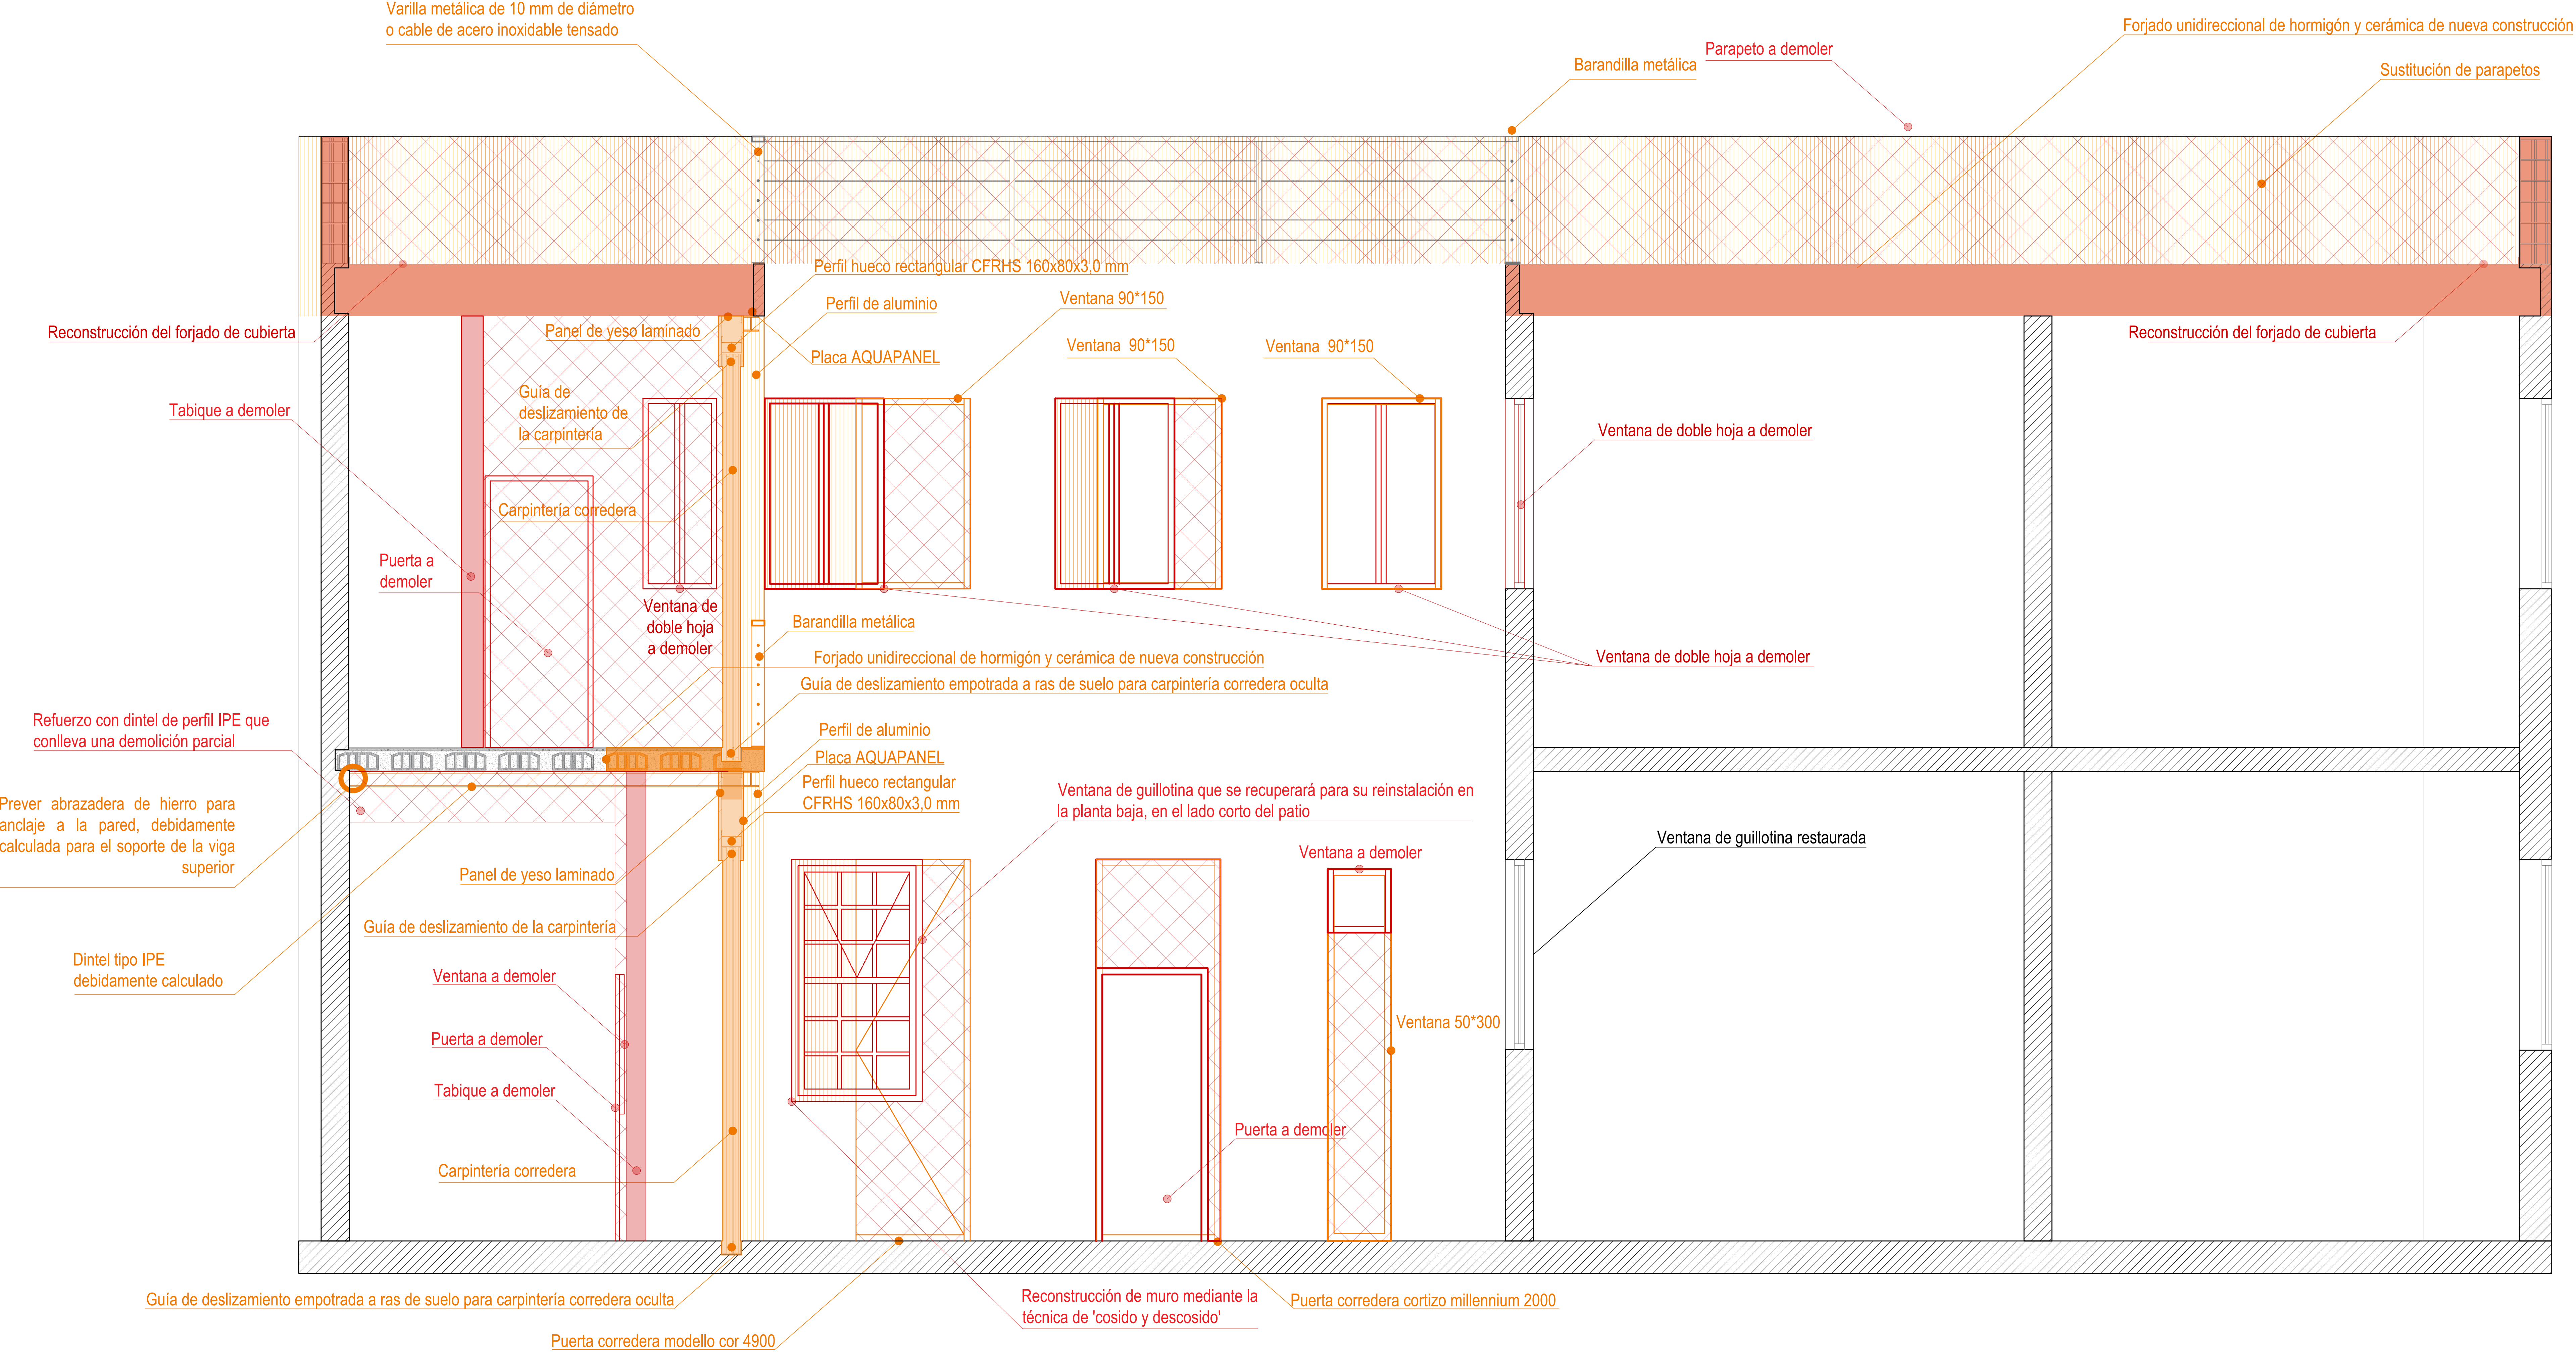


DETALLE APERTURA CARPINTERÍAS

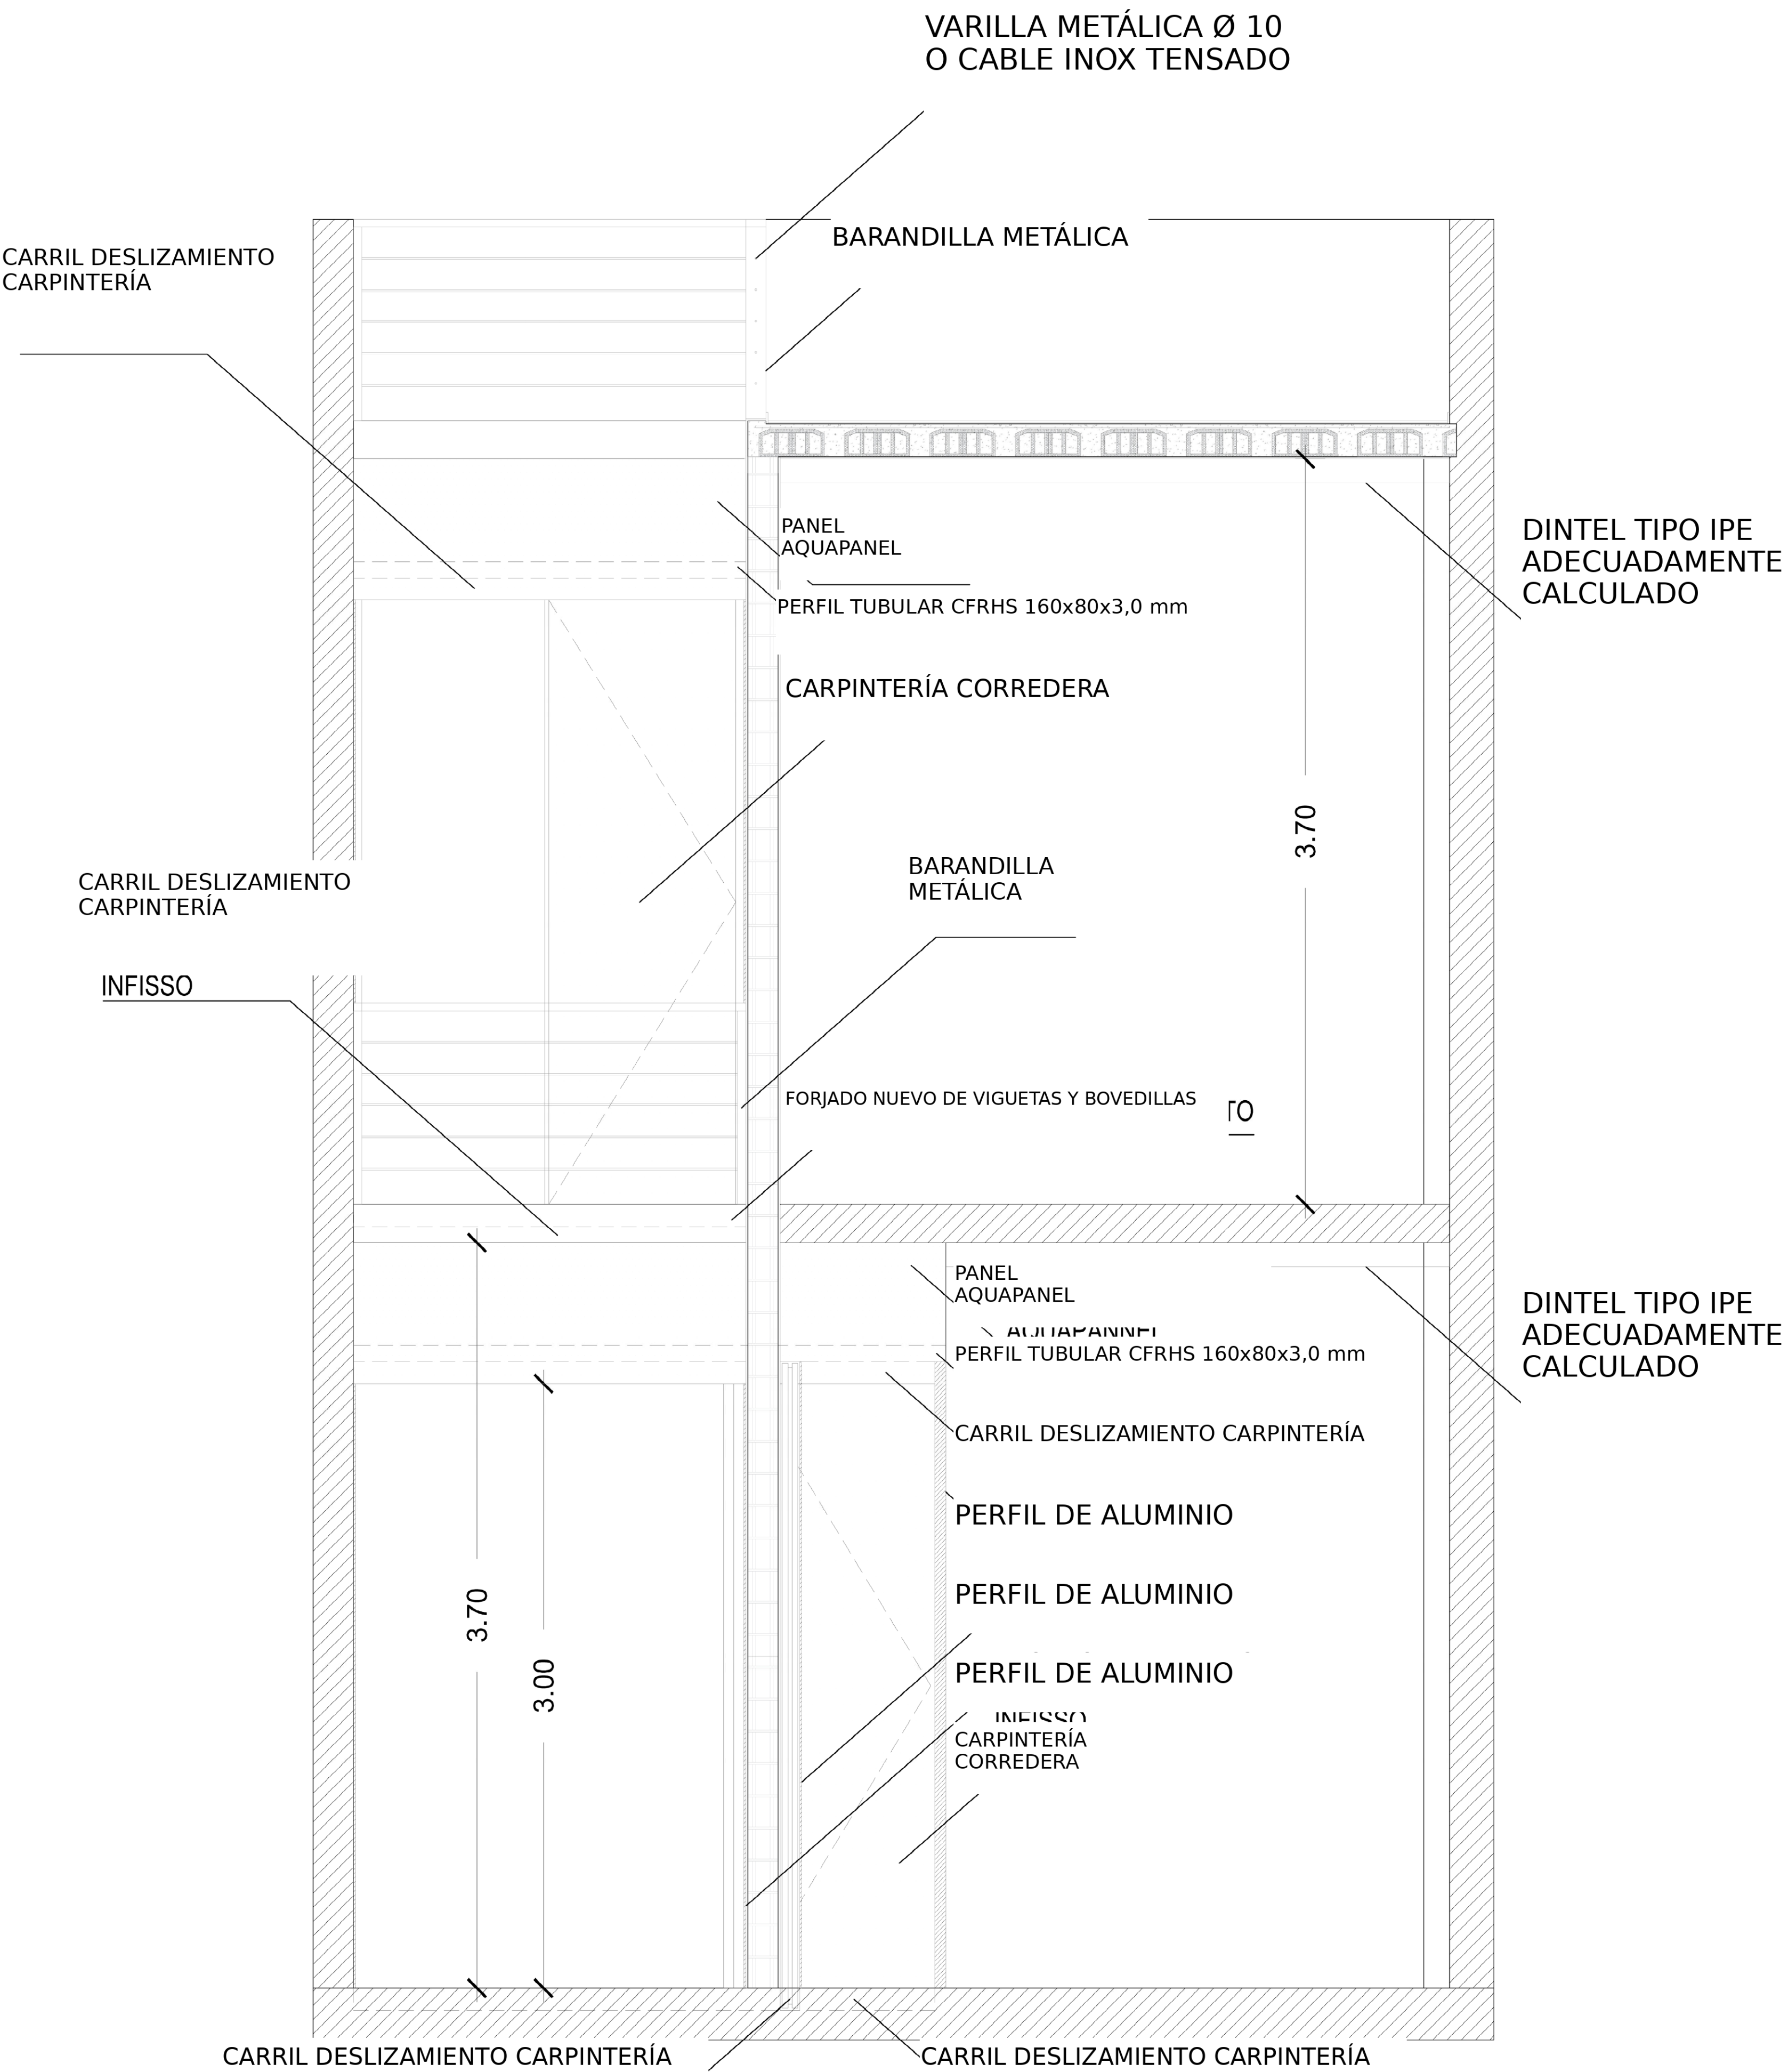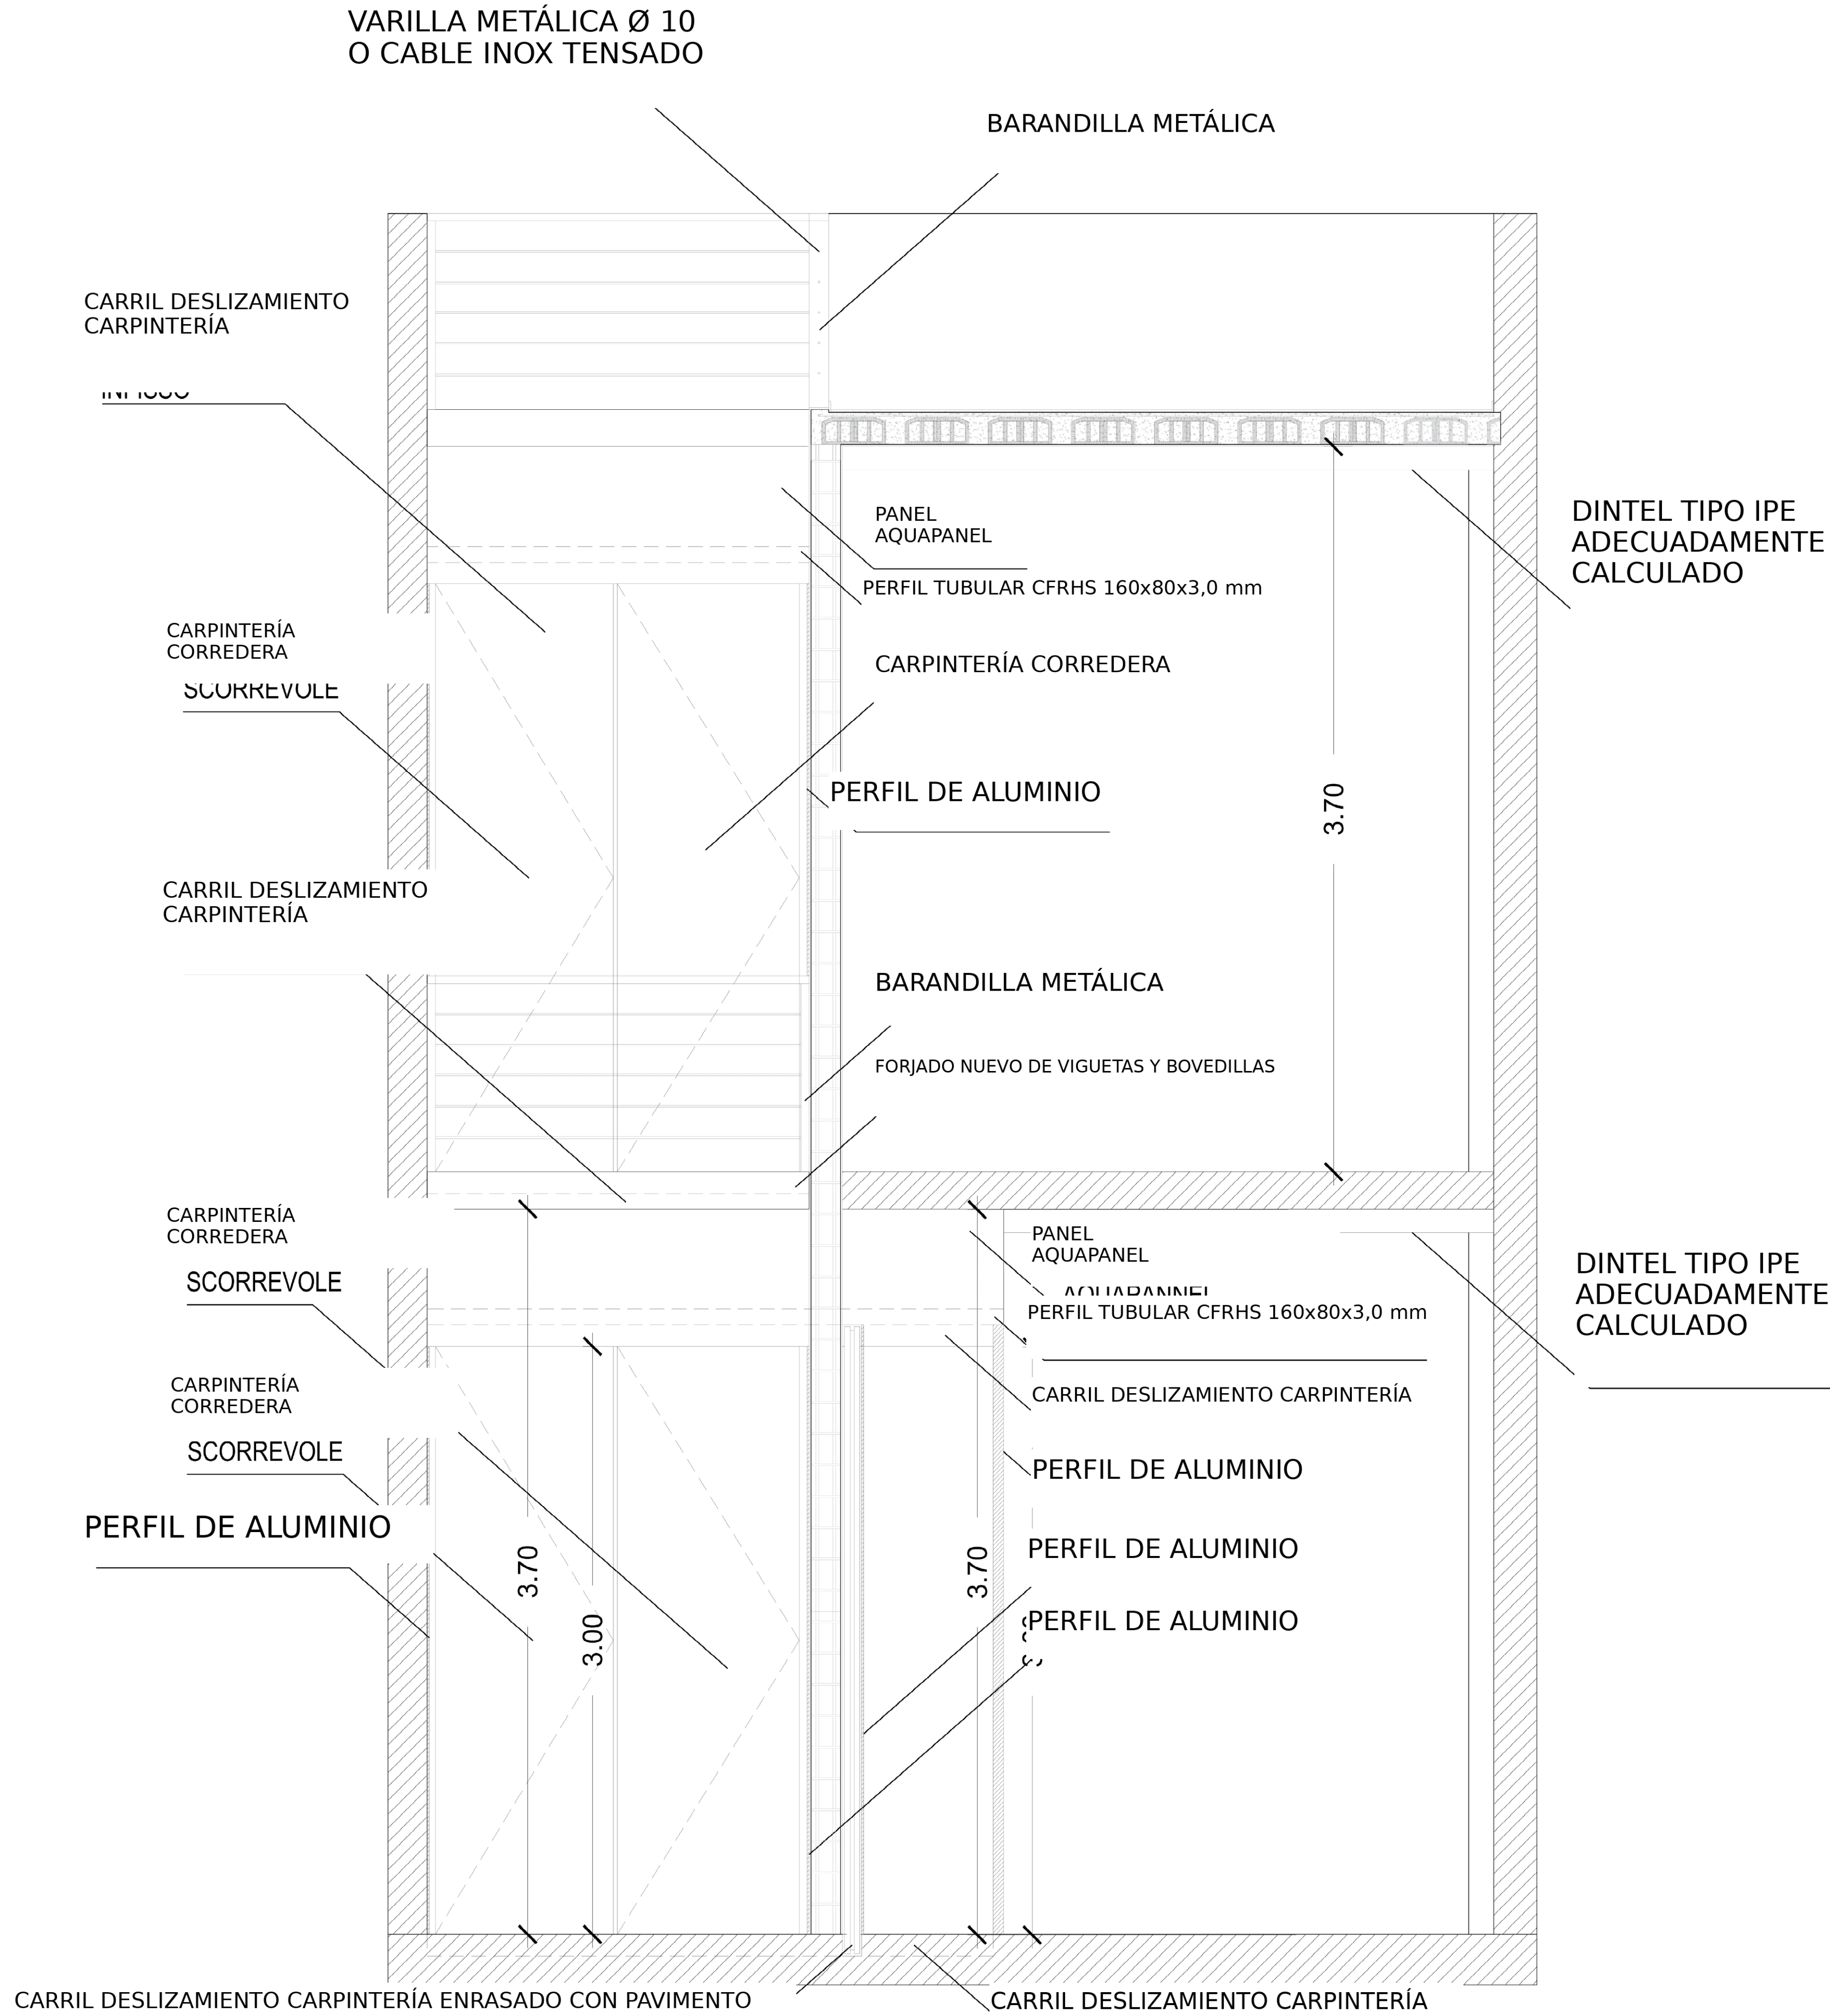

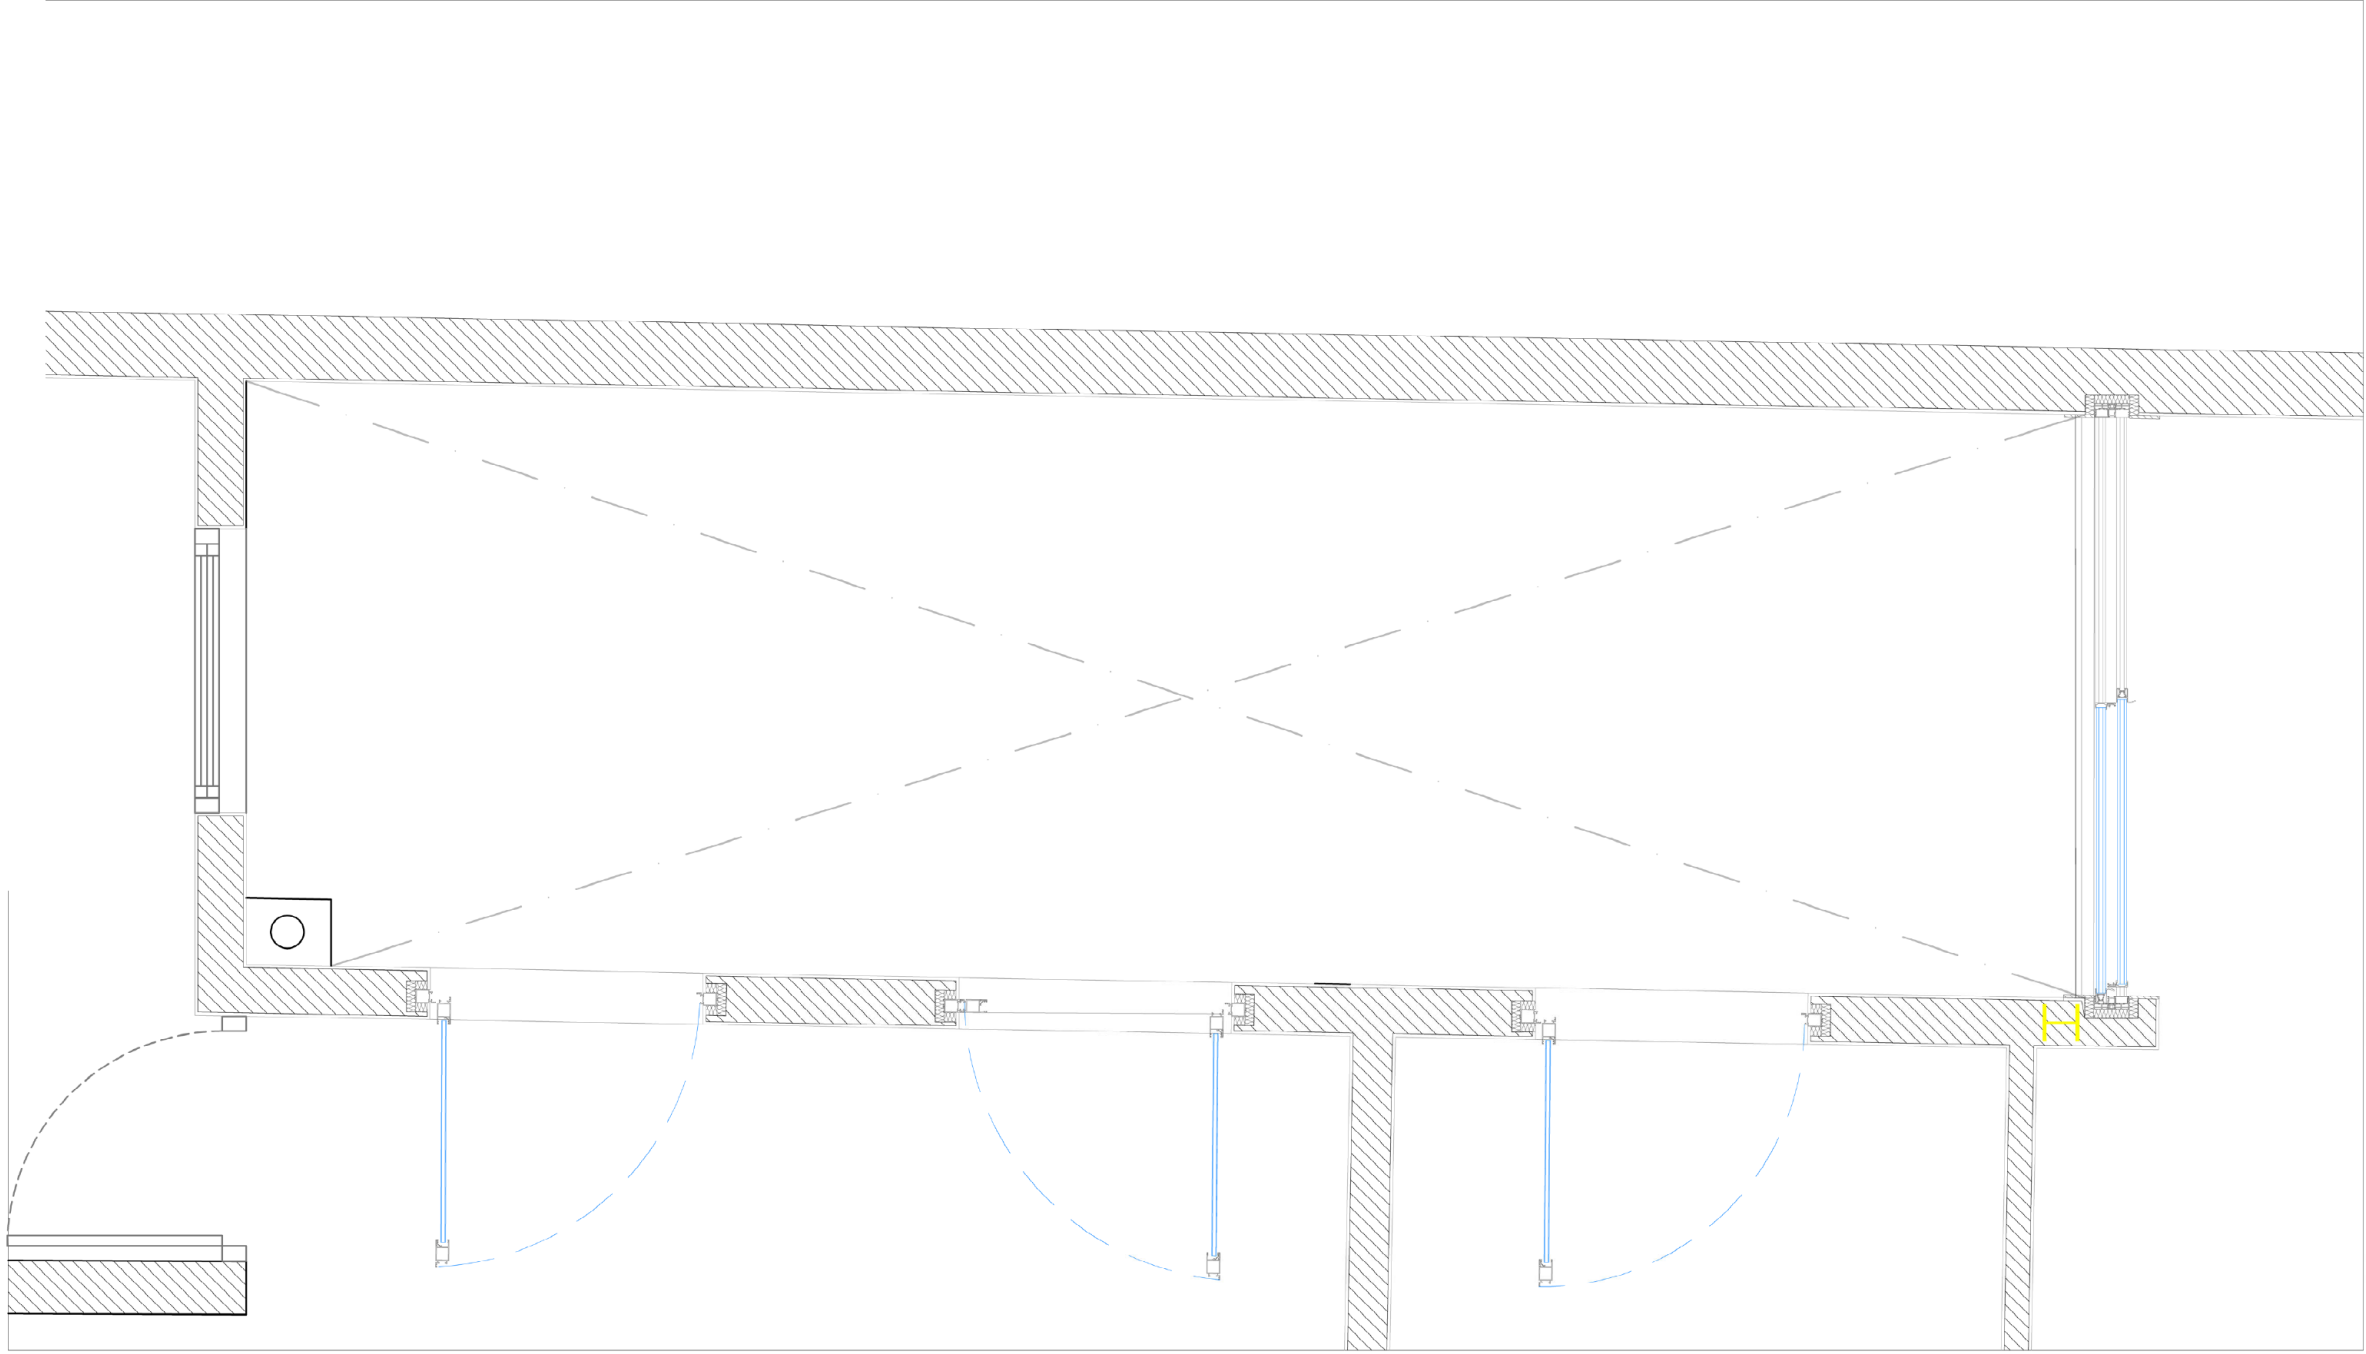

51
DETALE APERTURA CANTIEREAS

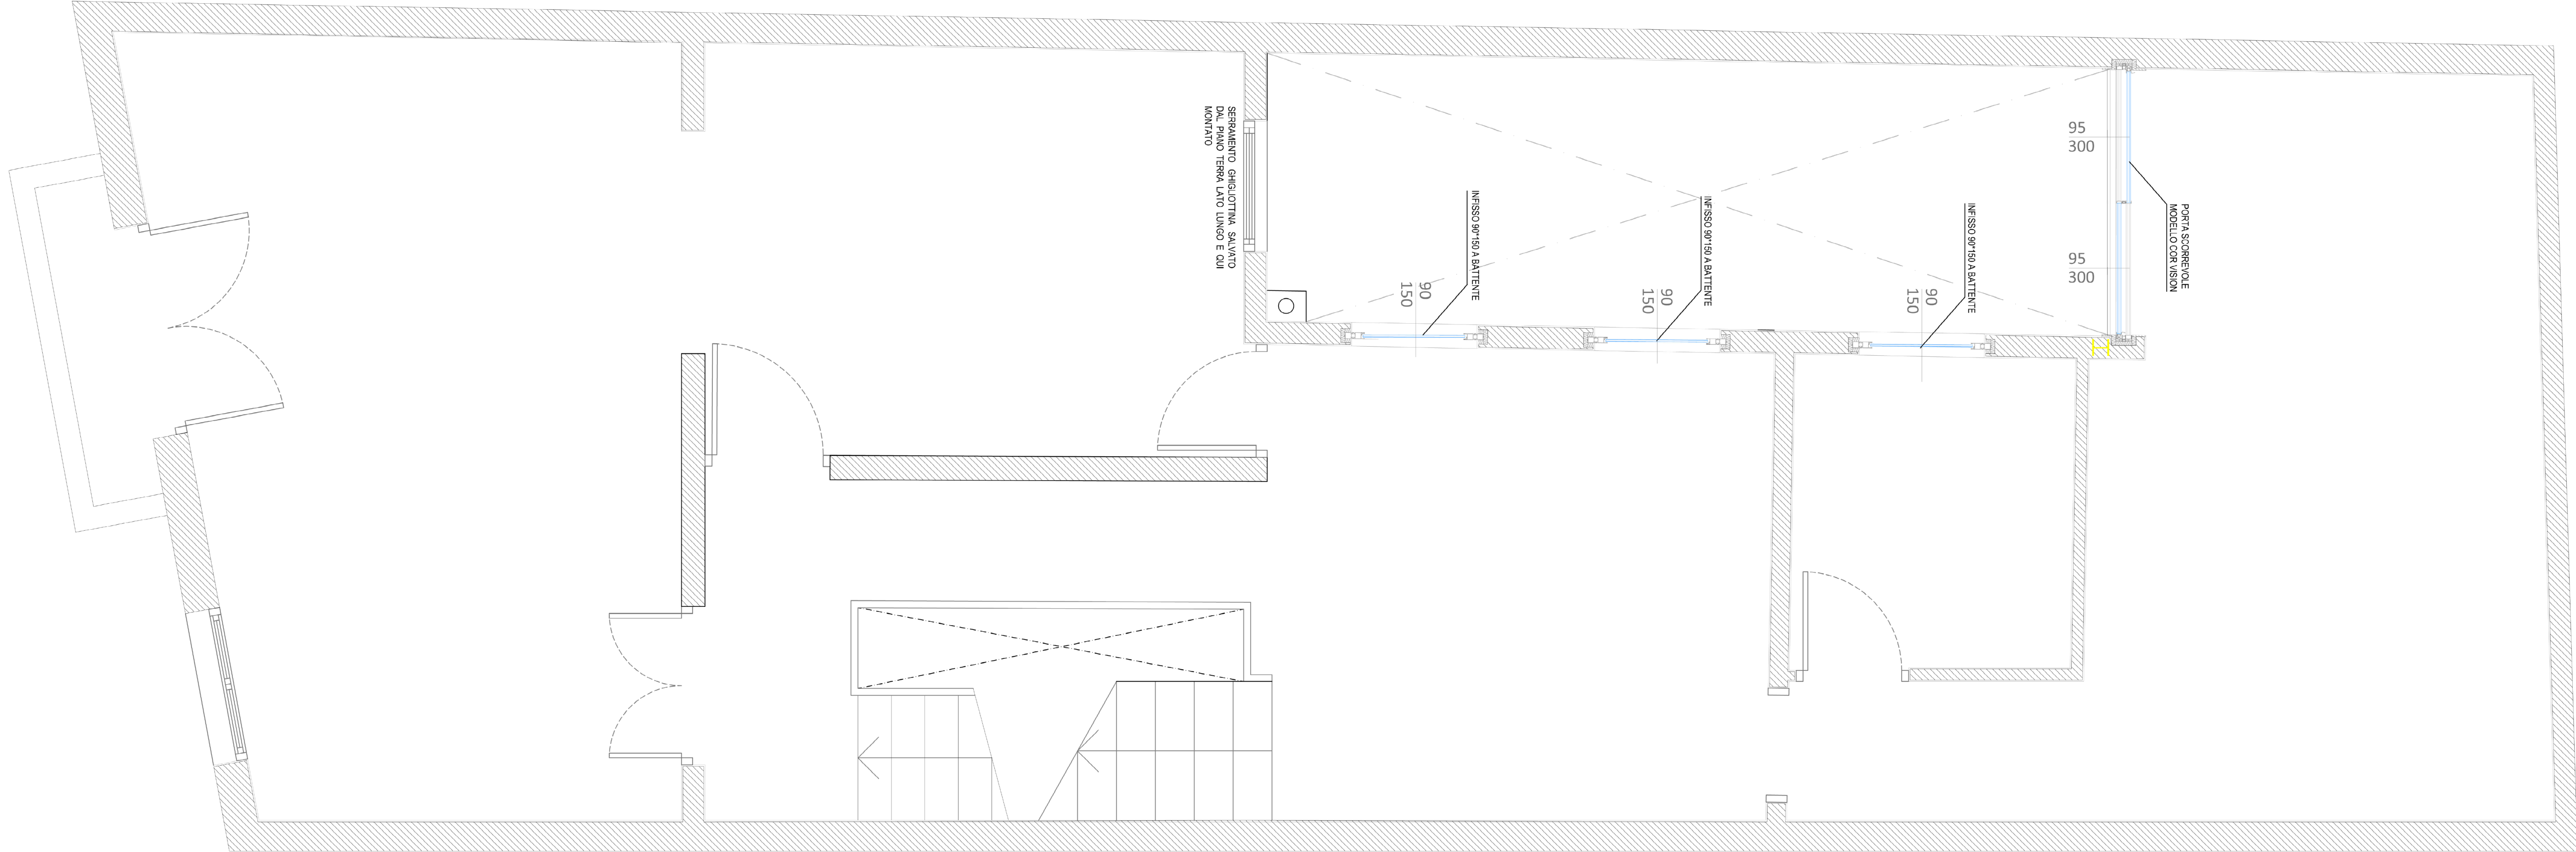

PORTA SCORREVOLE
MODELLO COR VISION

95 300

INFISSO 90° 150 A BATTENTE

90

150

INFISSO 90° 150 A BATTENTE

90


150

INFISSO 90° 150 A BATTENTE


90

150

SERRAMENTO GHISLOTINA SALVATO
DEL PIANO TERRA LATO LUNGO E CUI
MONTATO

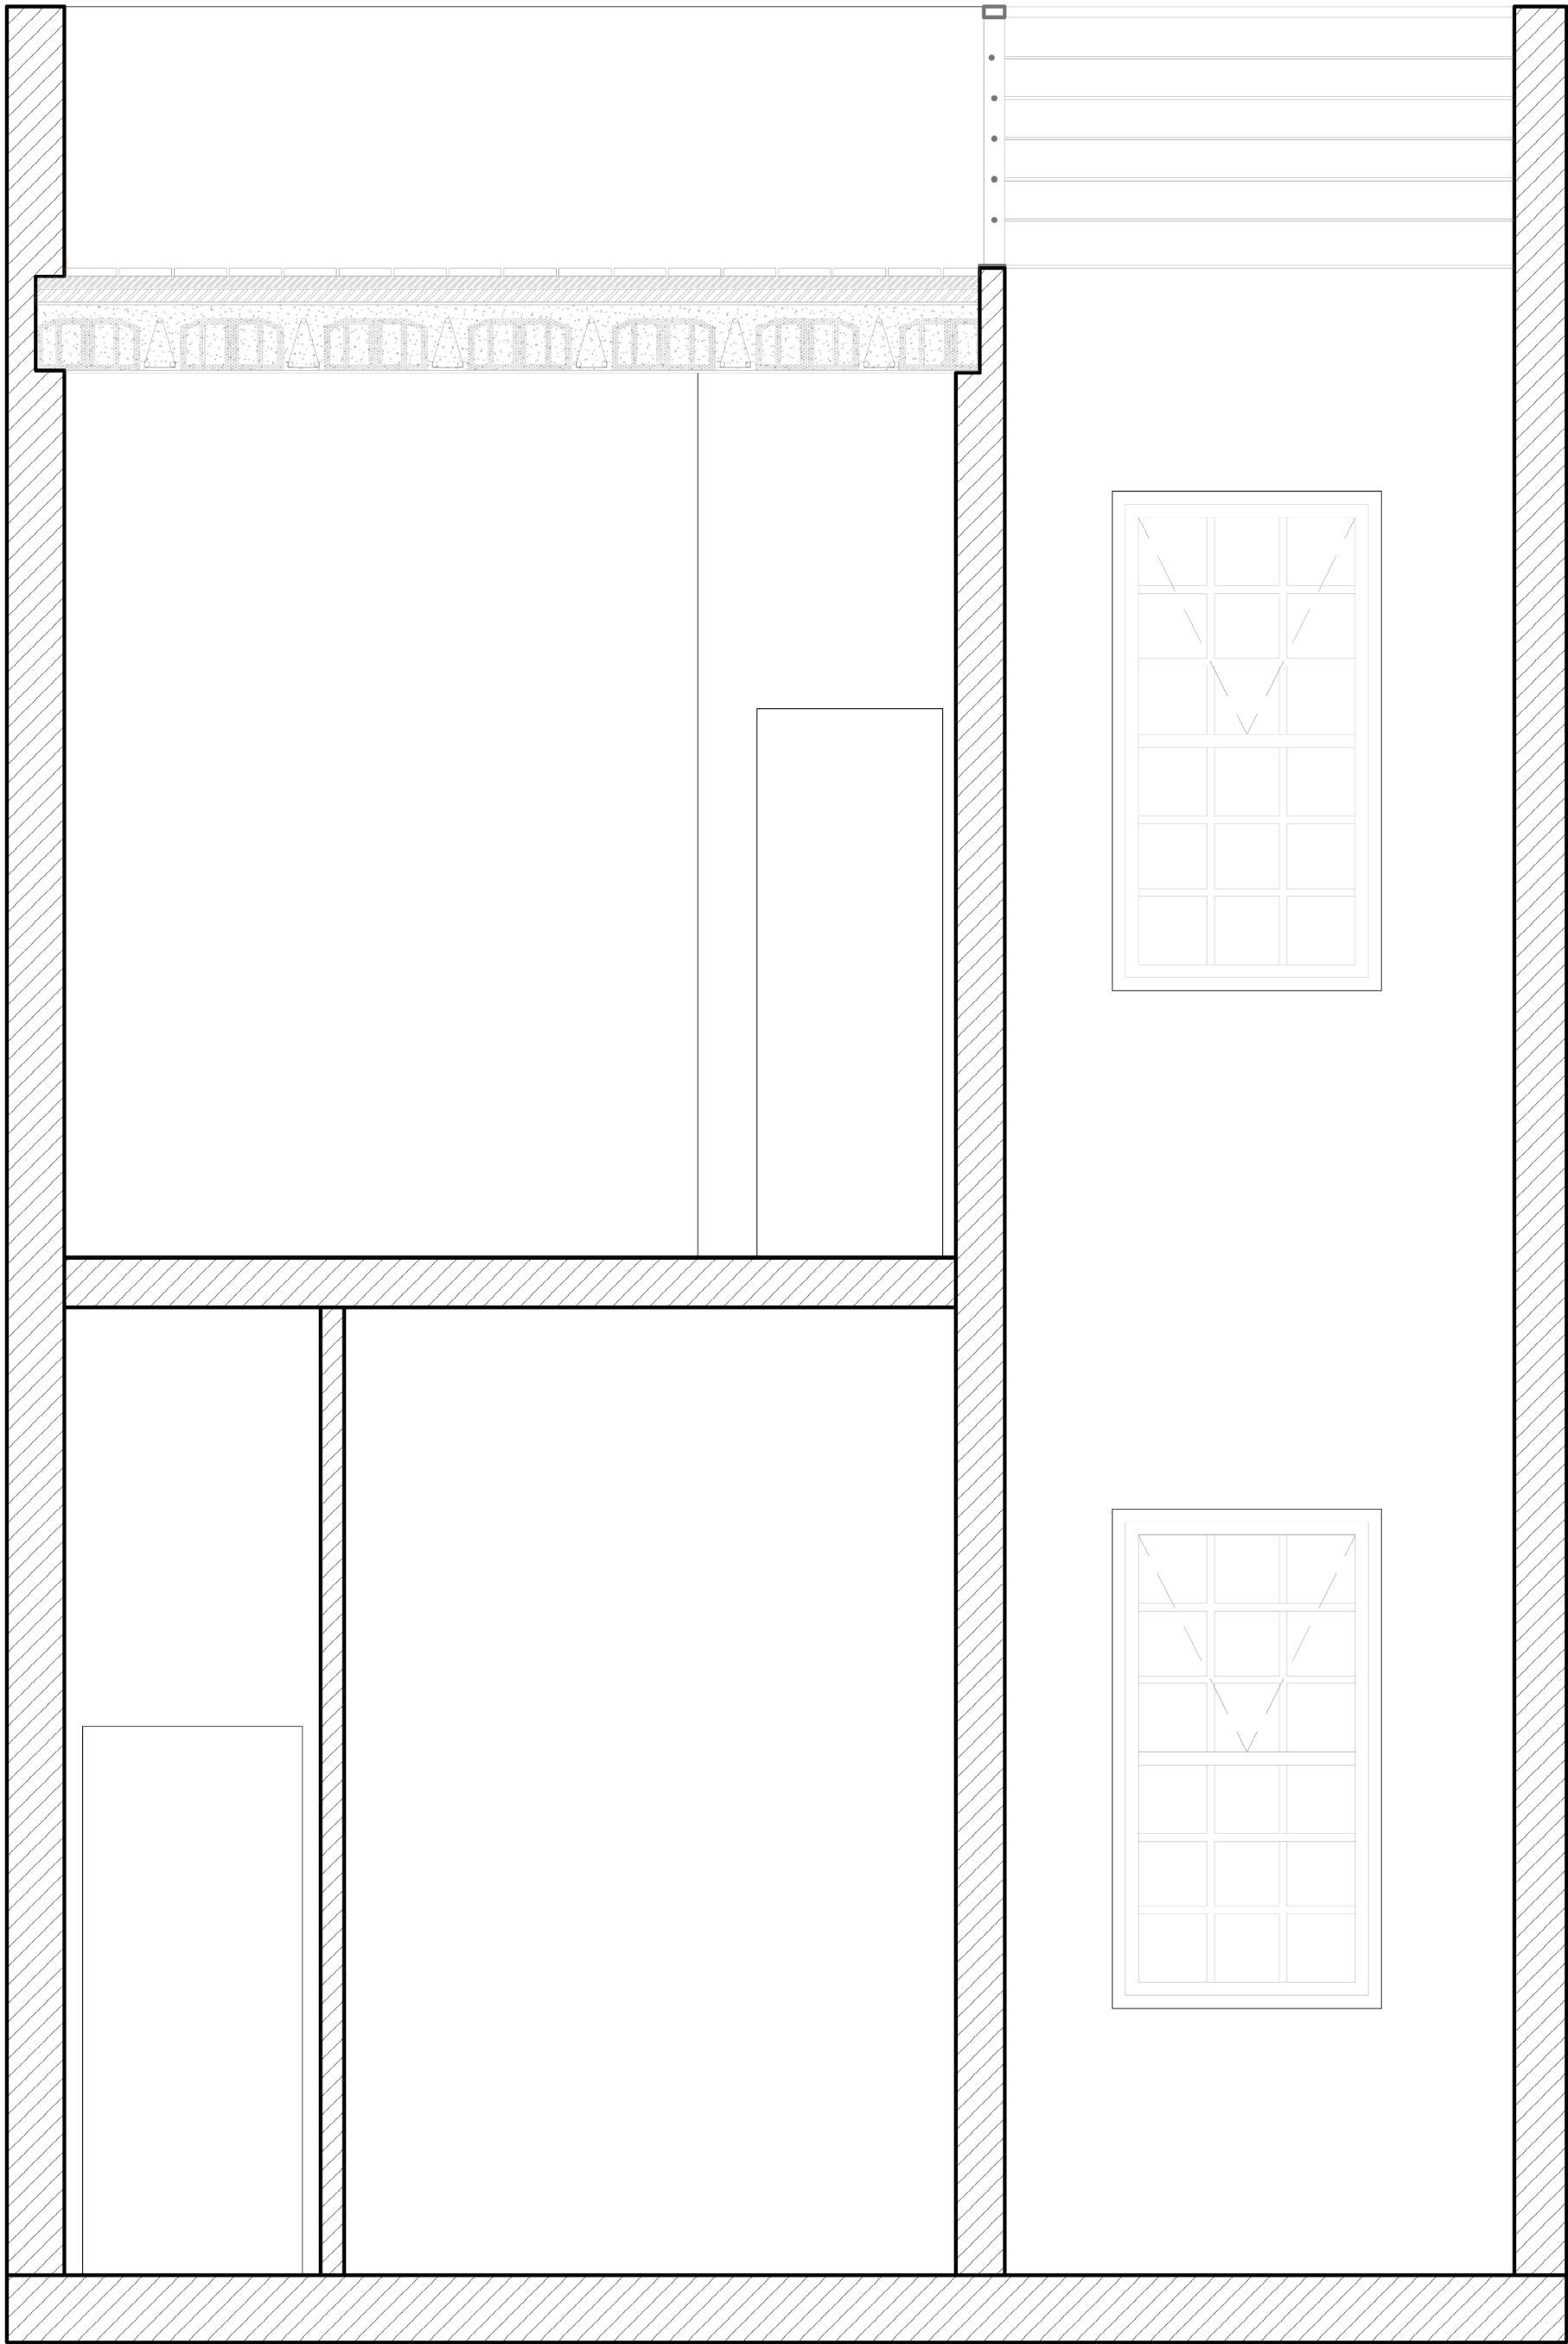


ALZADO NORTE

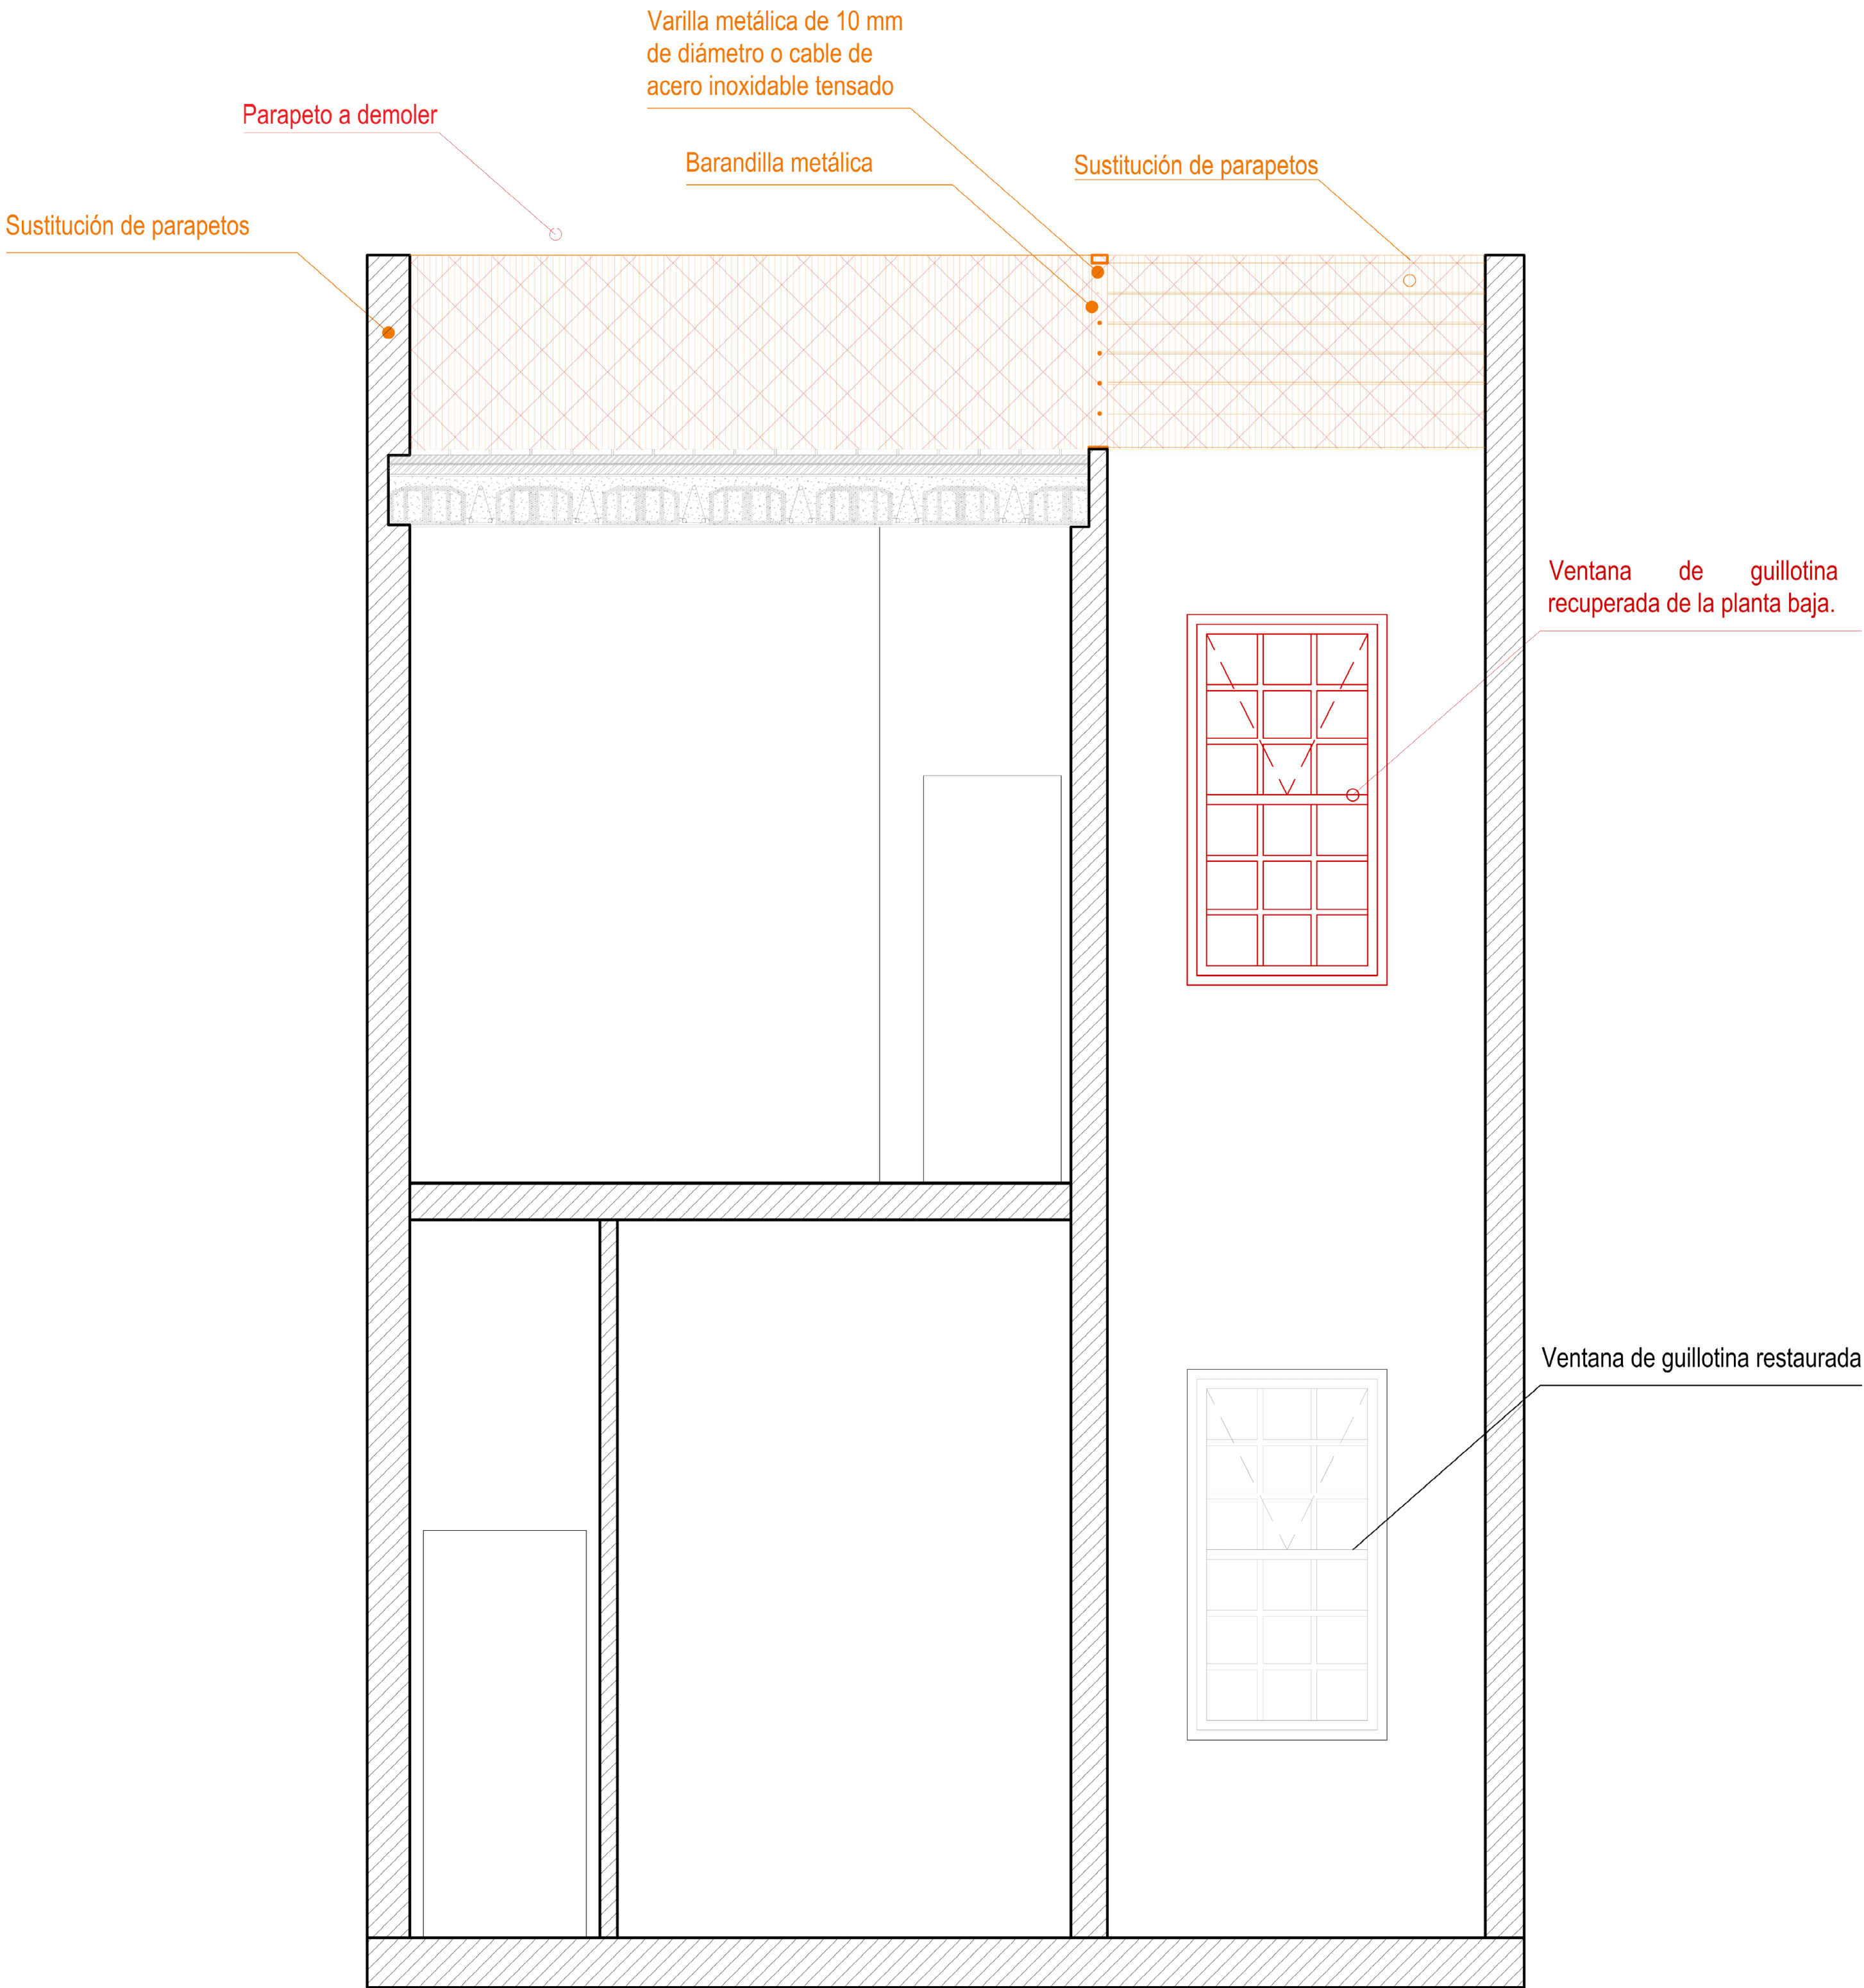


CONSTRUCCIÓN CONSTRUCCIÓN DE LA SUPERFICIE DEMOLICIÓN DEMOLICIÓN DE SUPERFICIES

ALZADO NORTE - CONSTRUCCIÓN Y DEMOLICIÓN

ESCALA 1:20

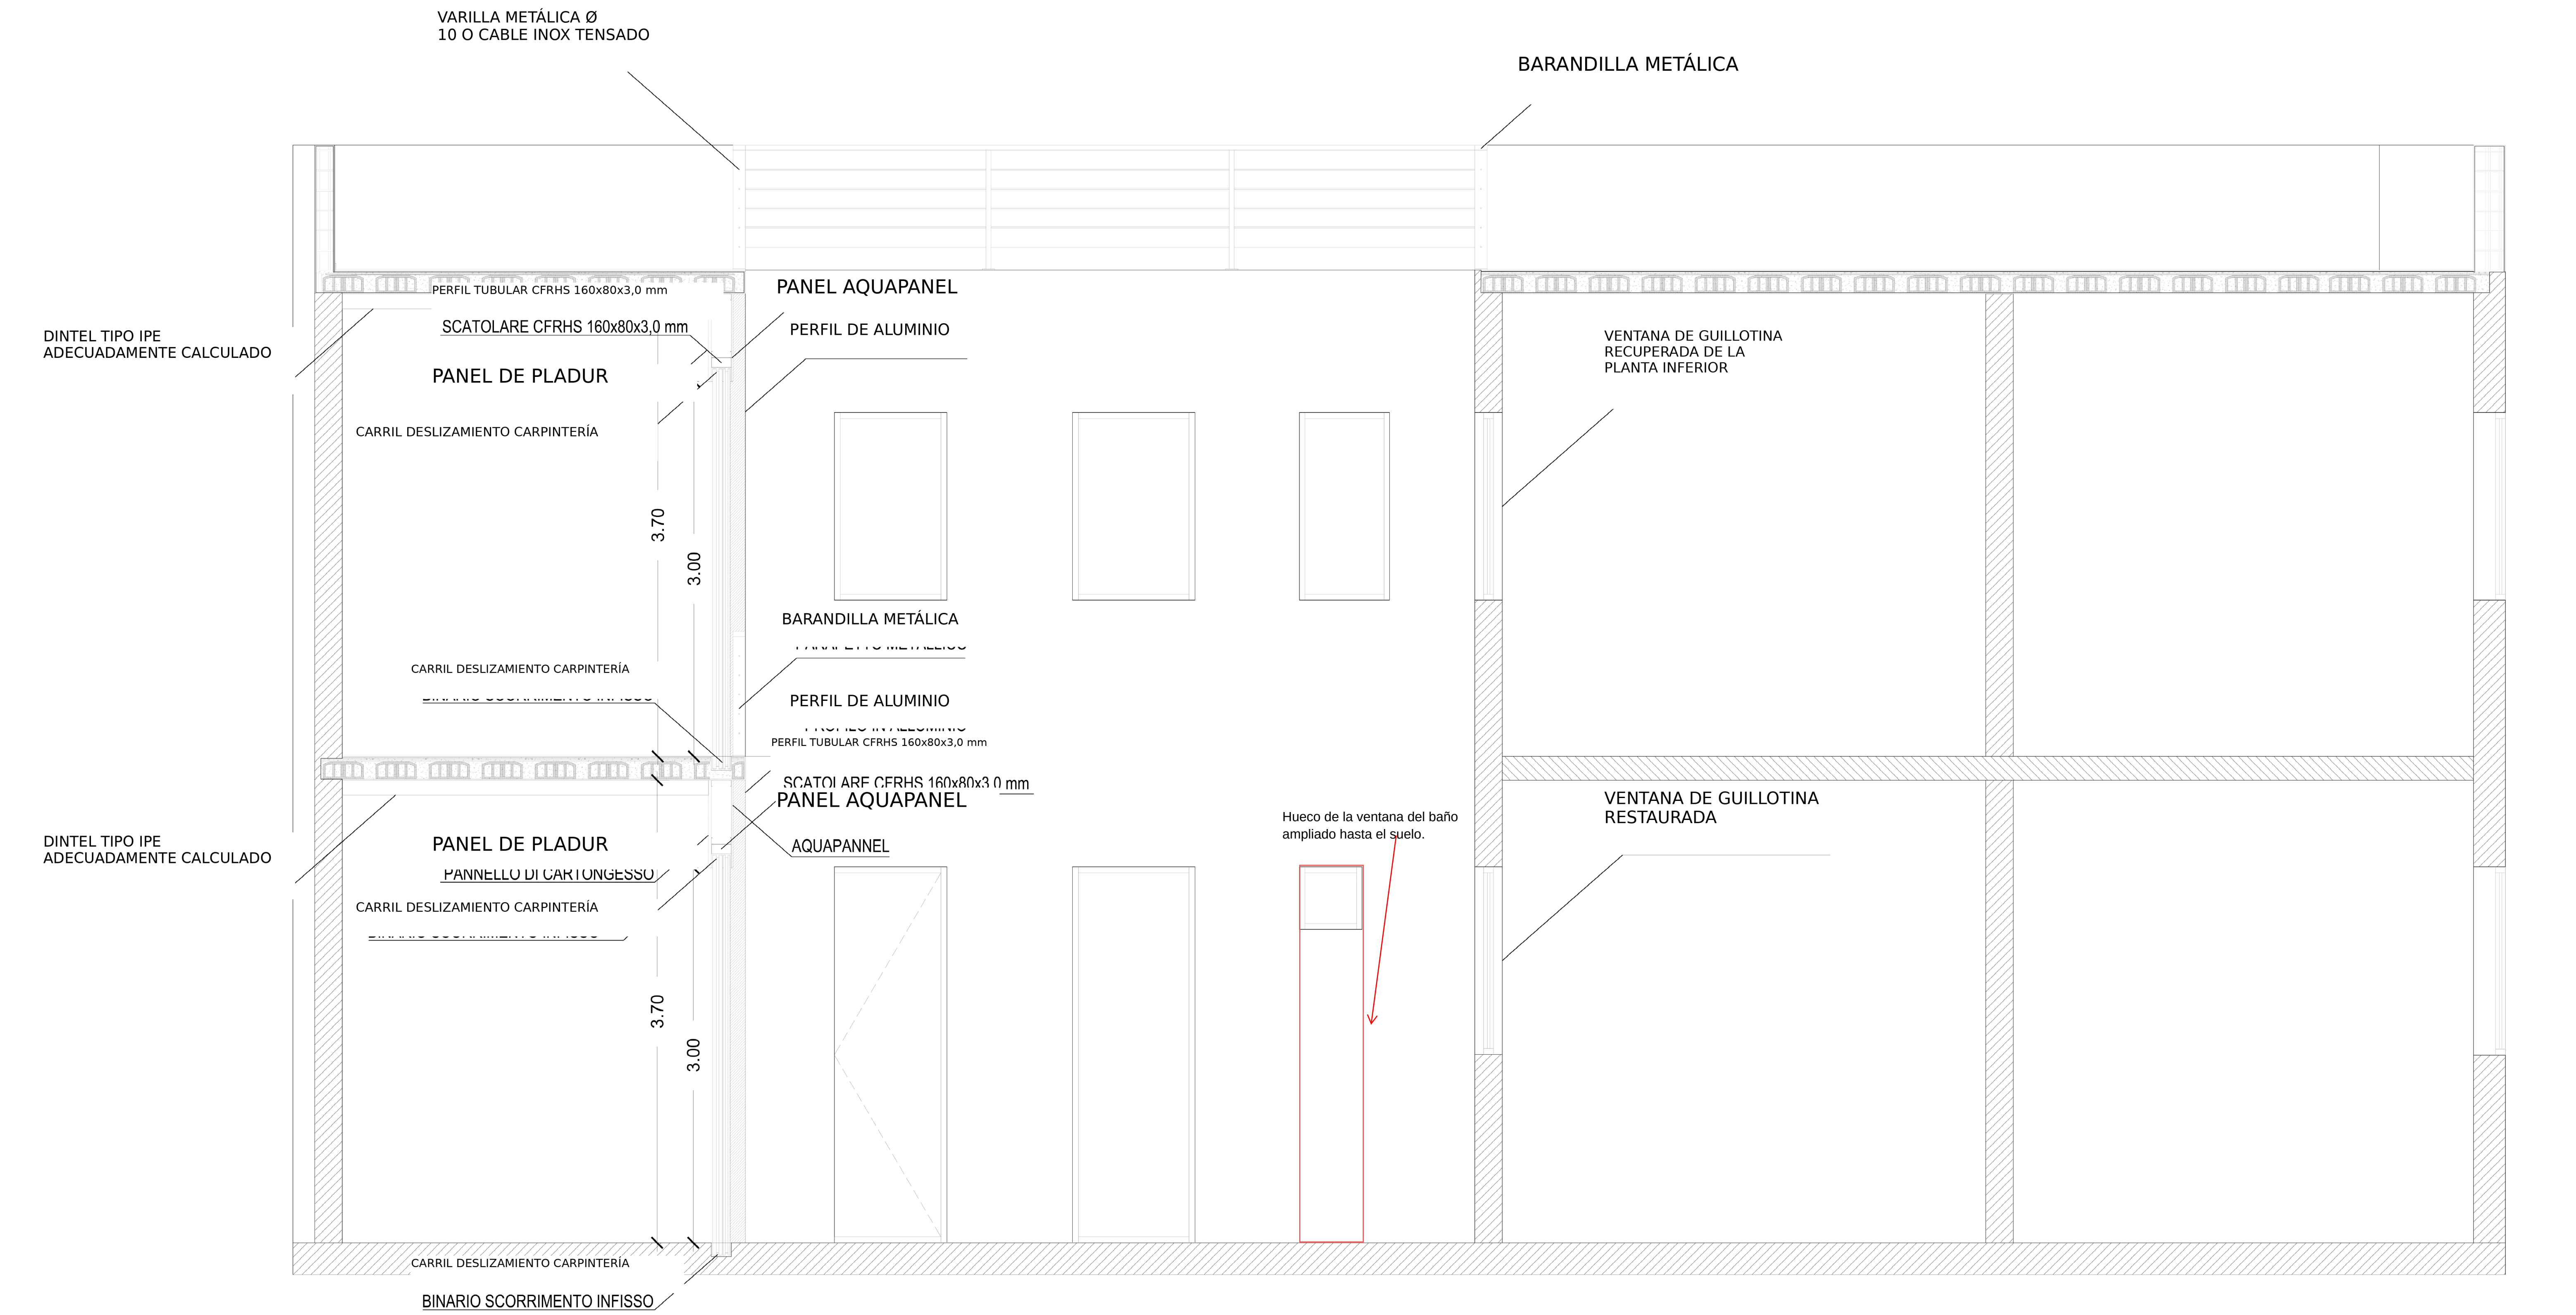

ALZADO OESTE

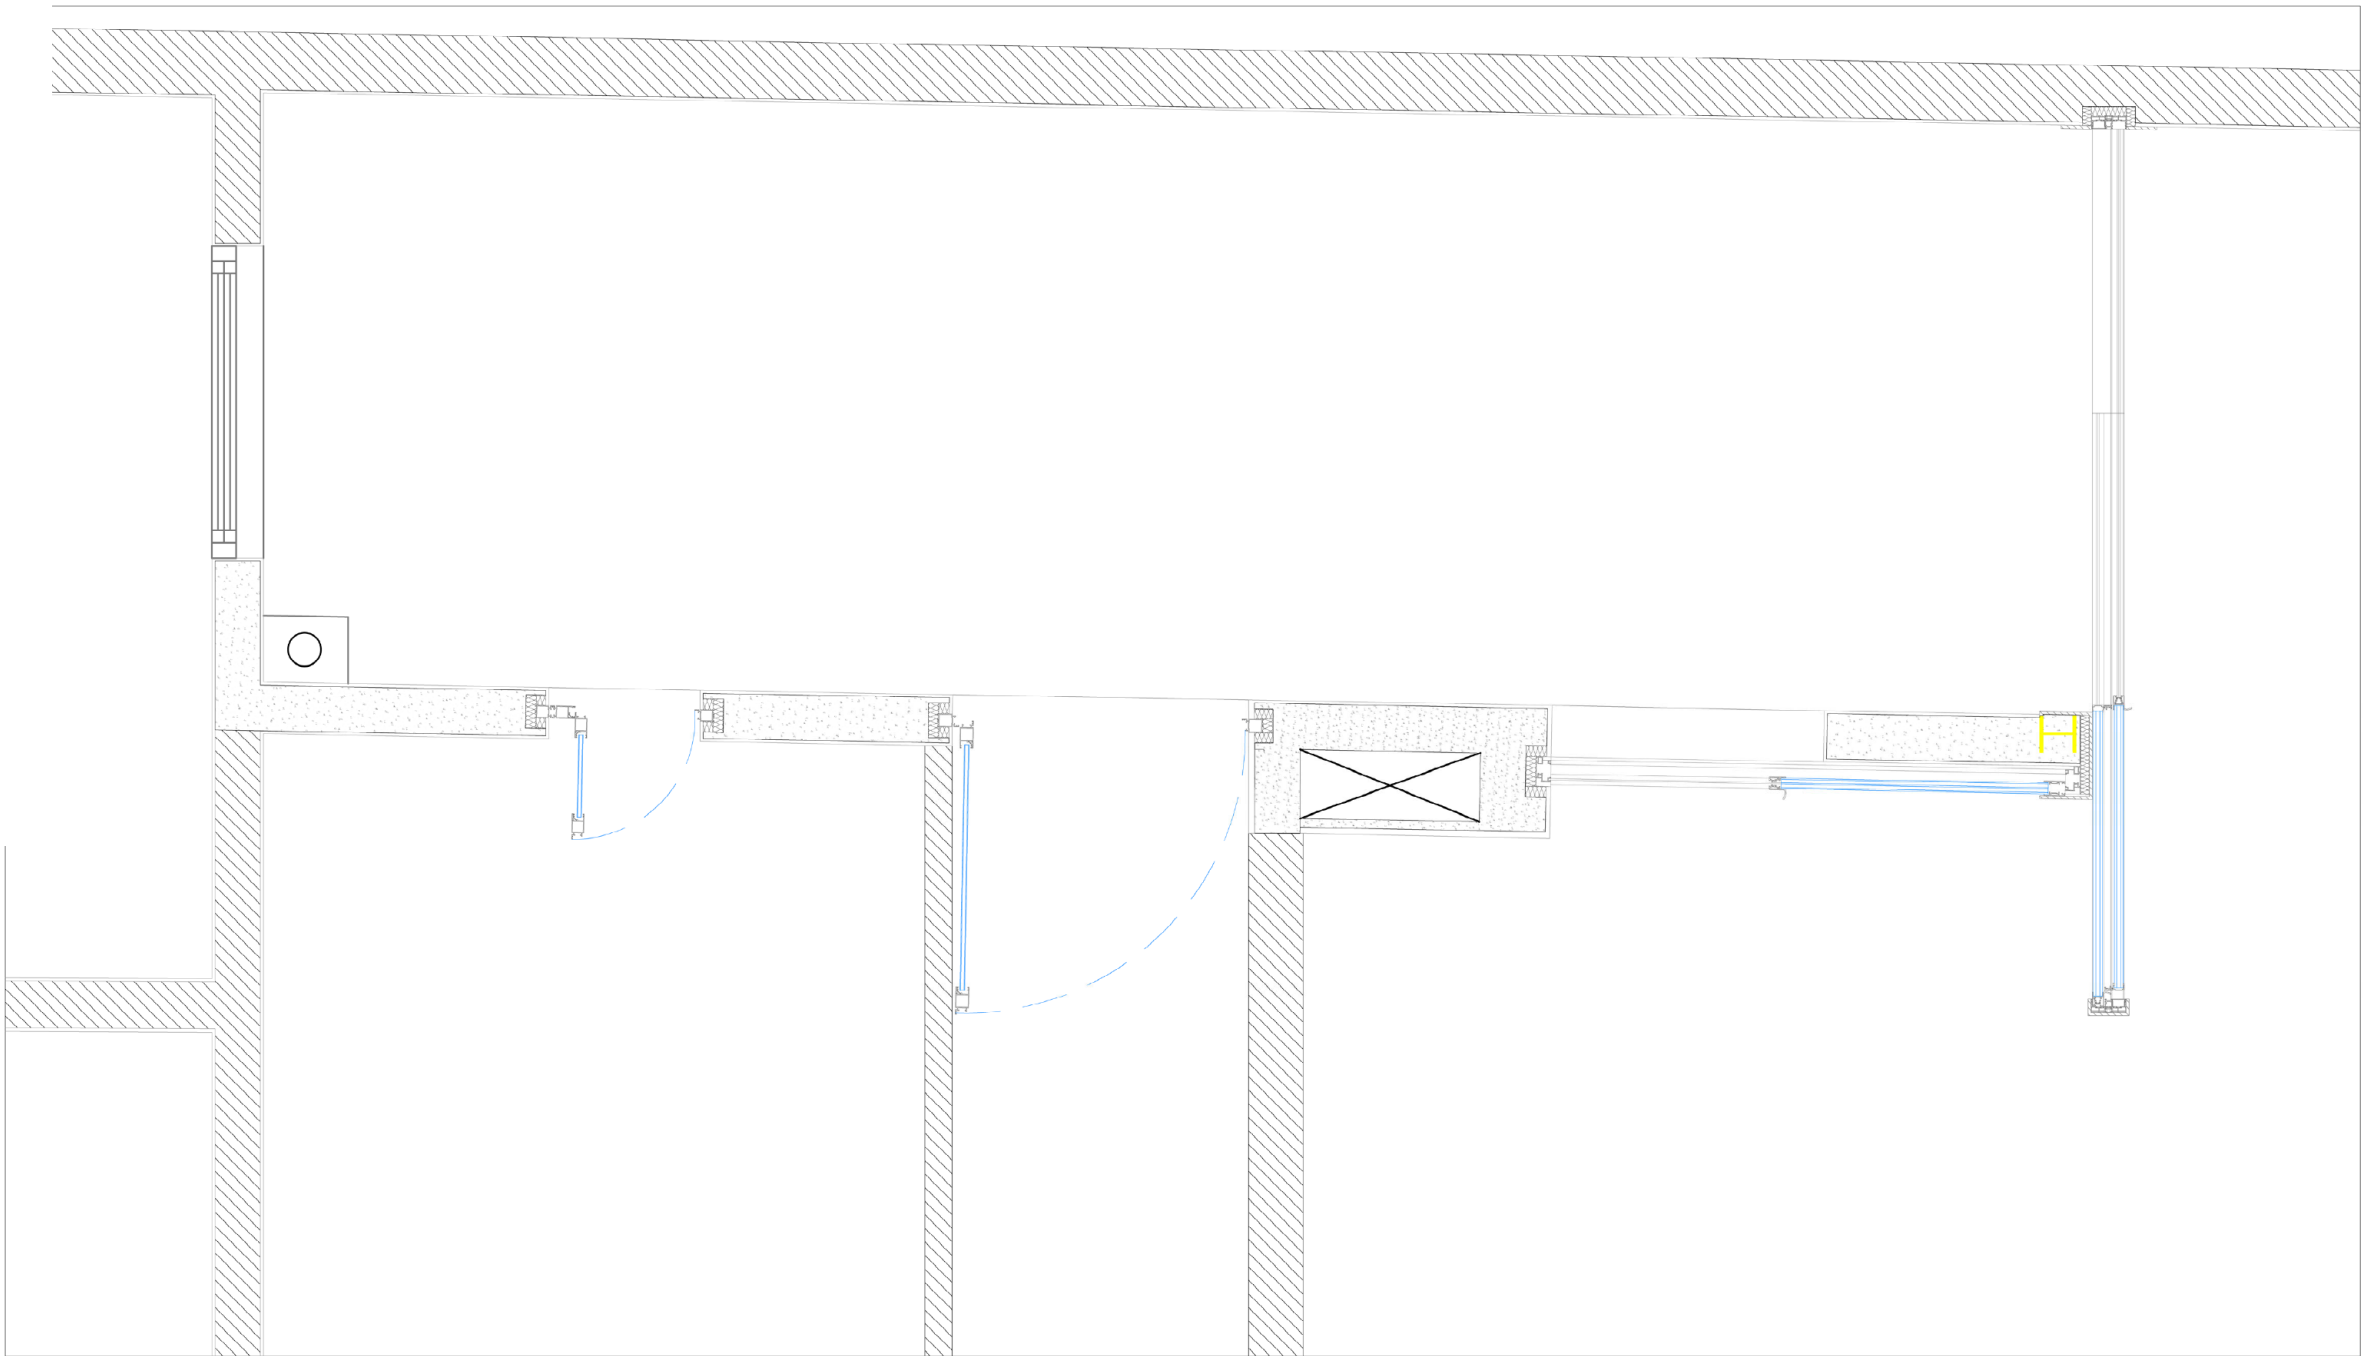

DETTAGLI APERTURA CARPENTERIAS

SSI

